


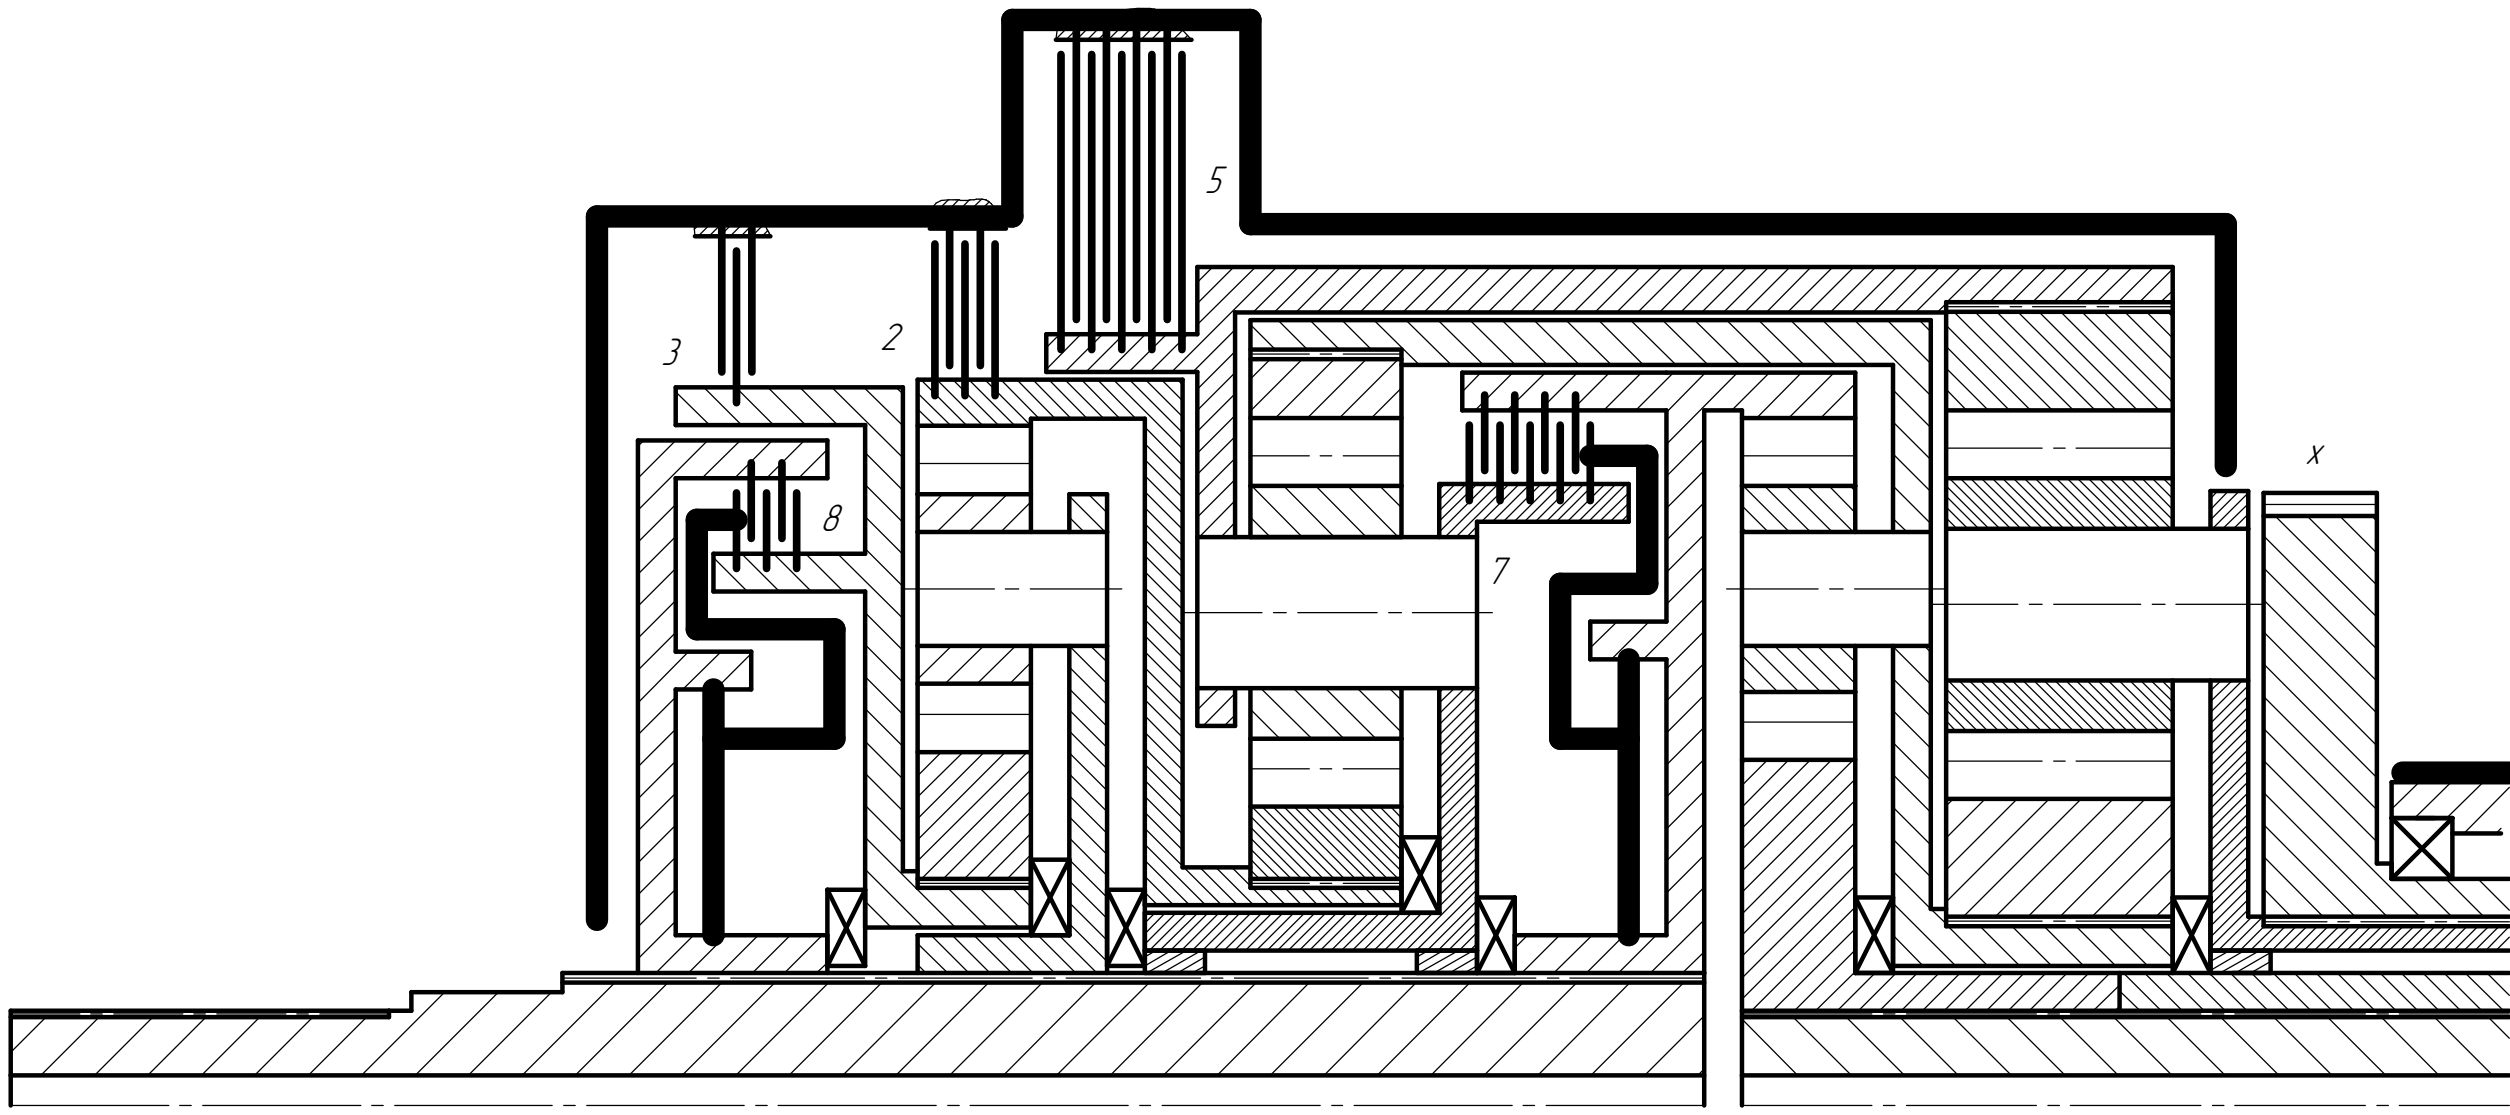
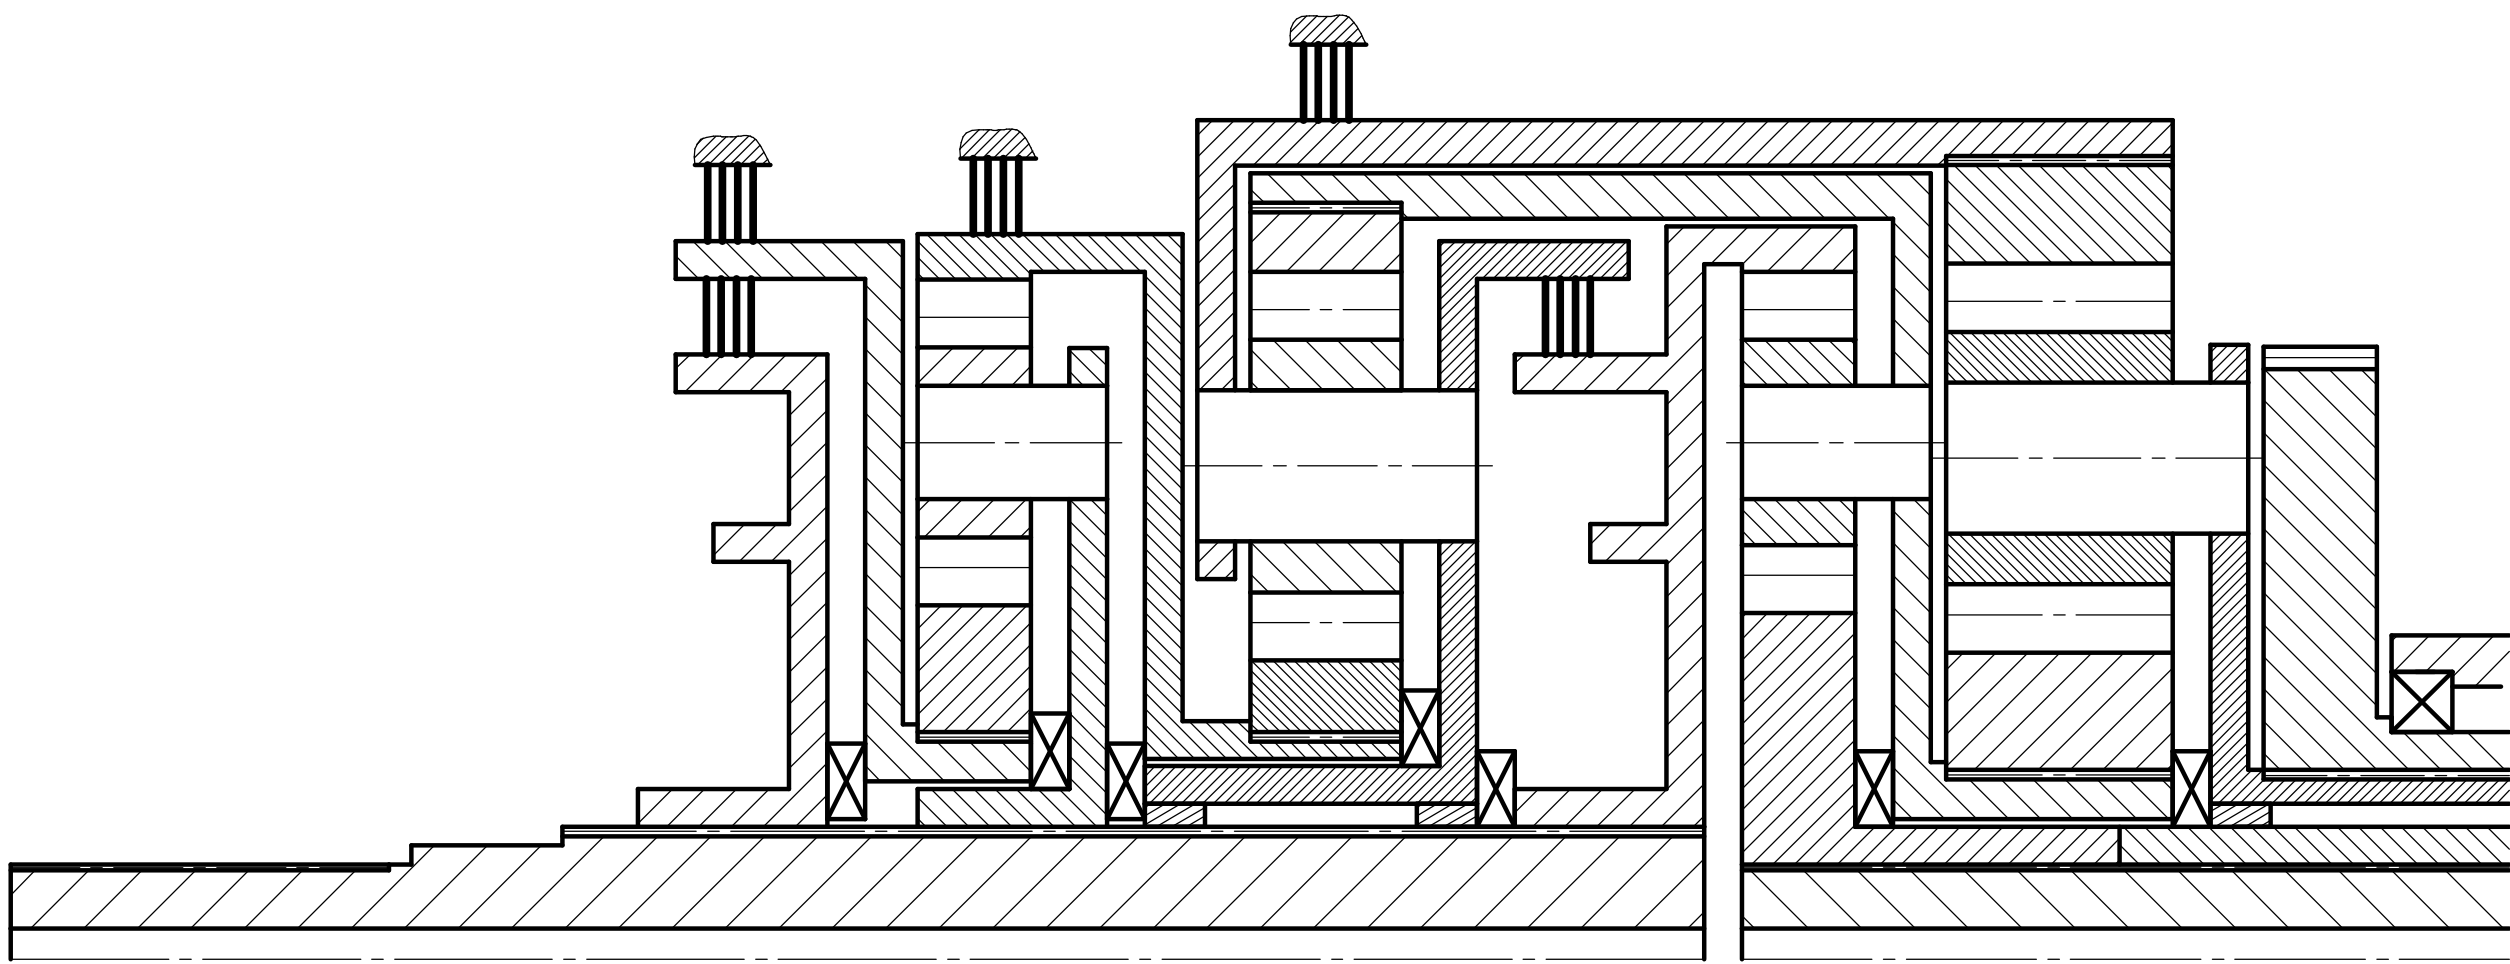
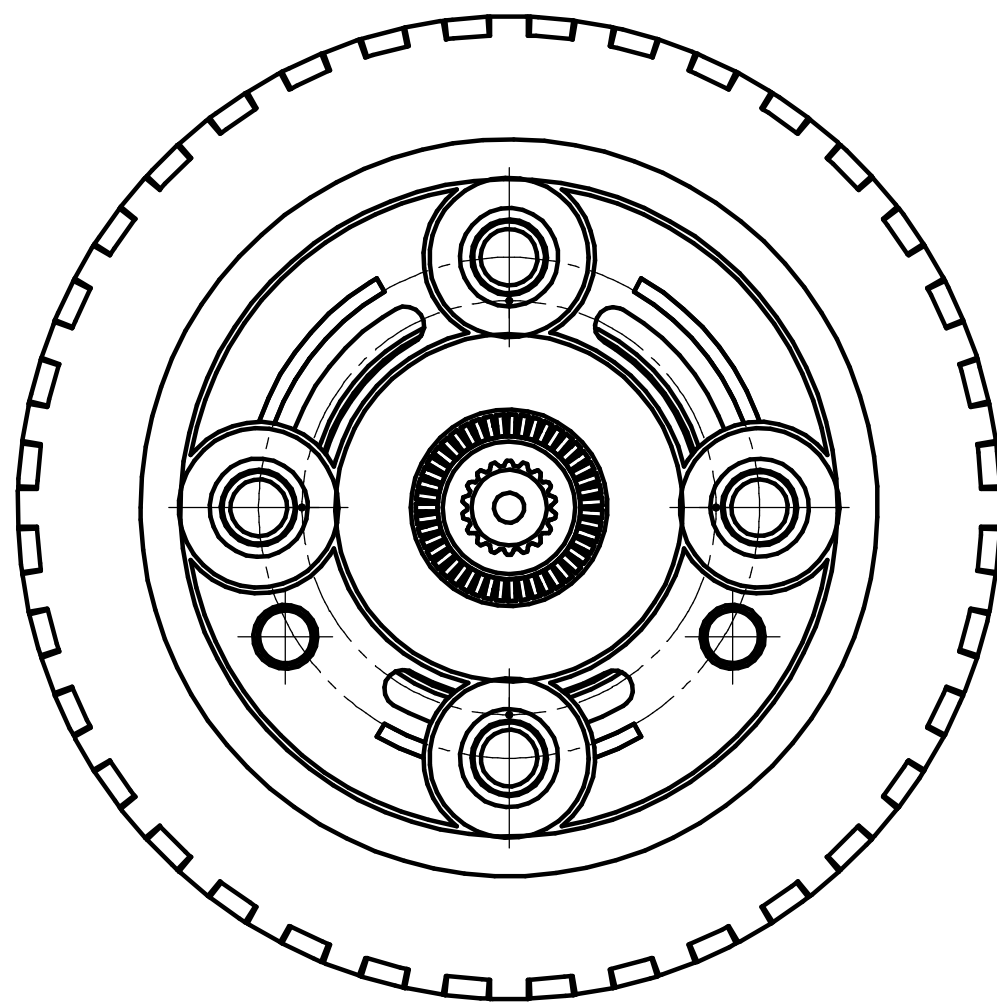
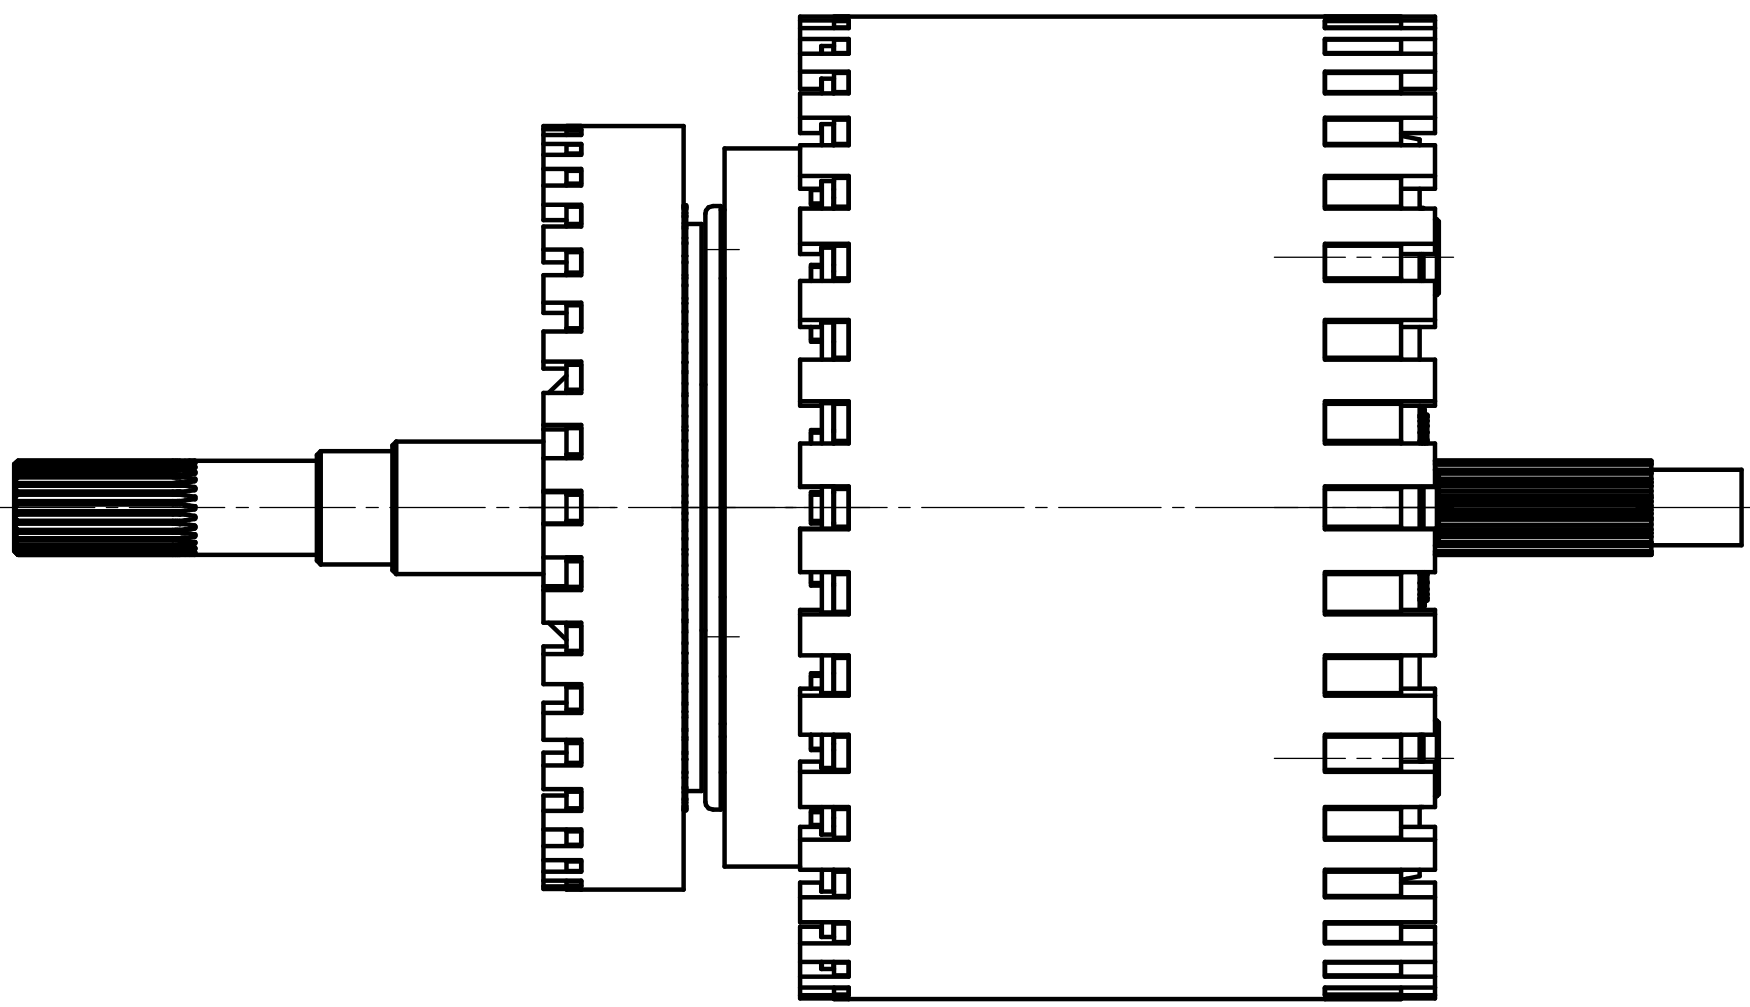


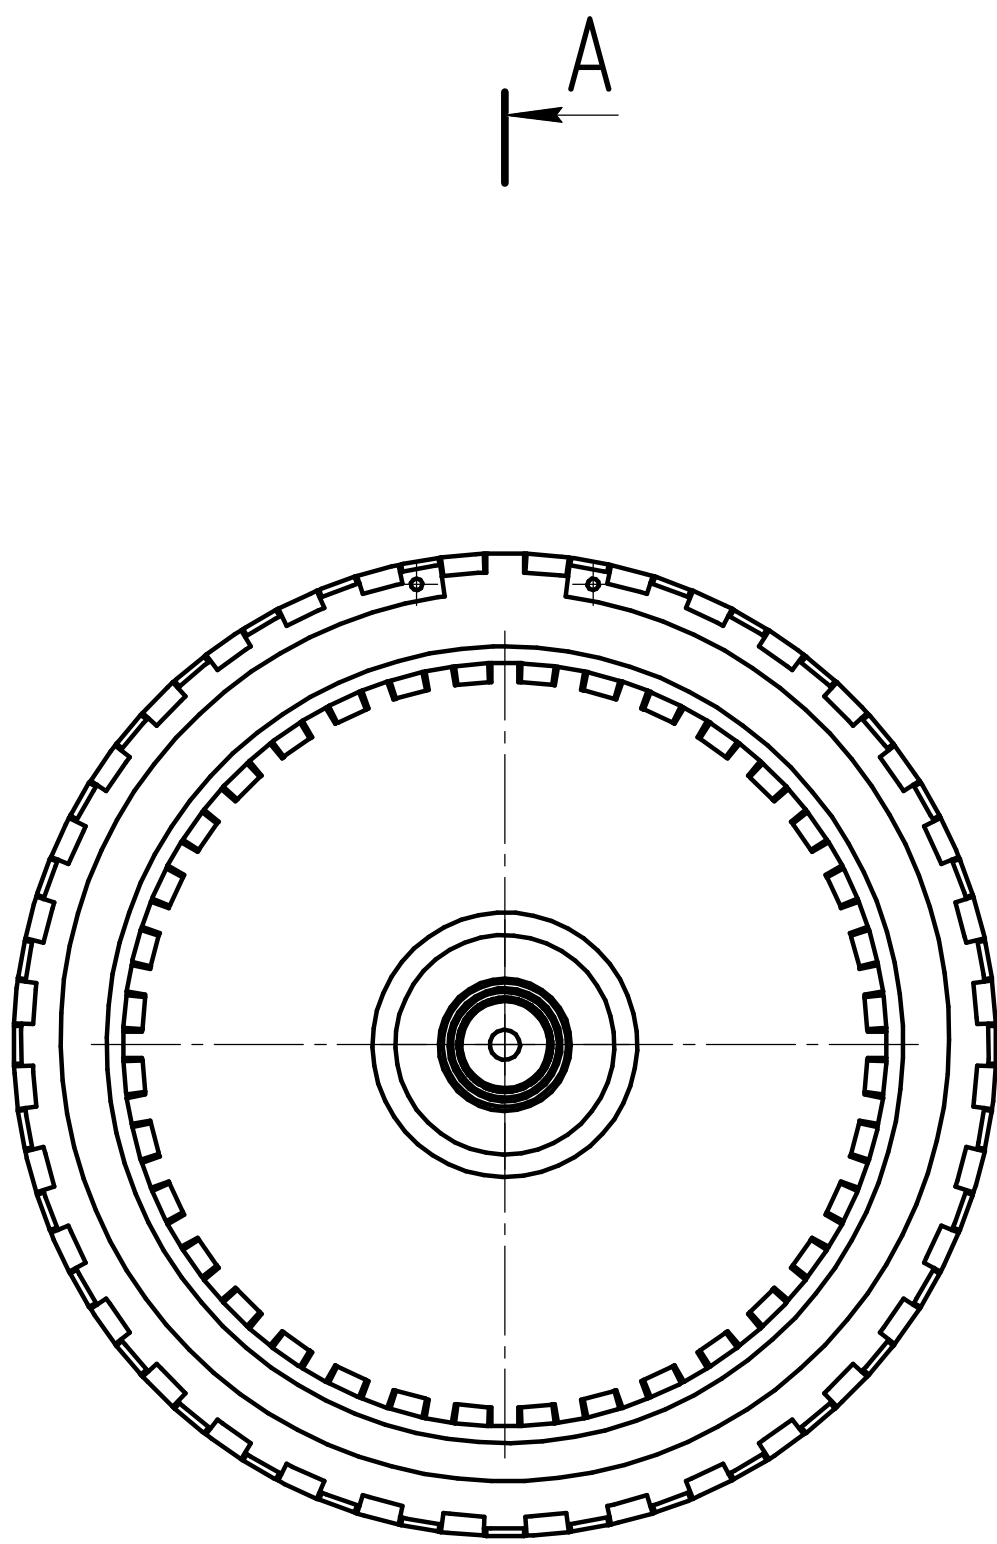

КПСМ 09.2026.05.000 СБ

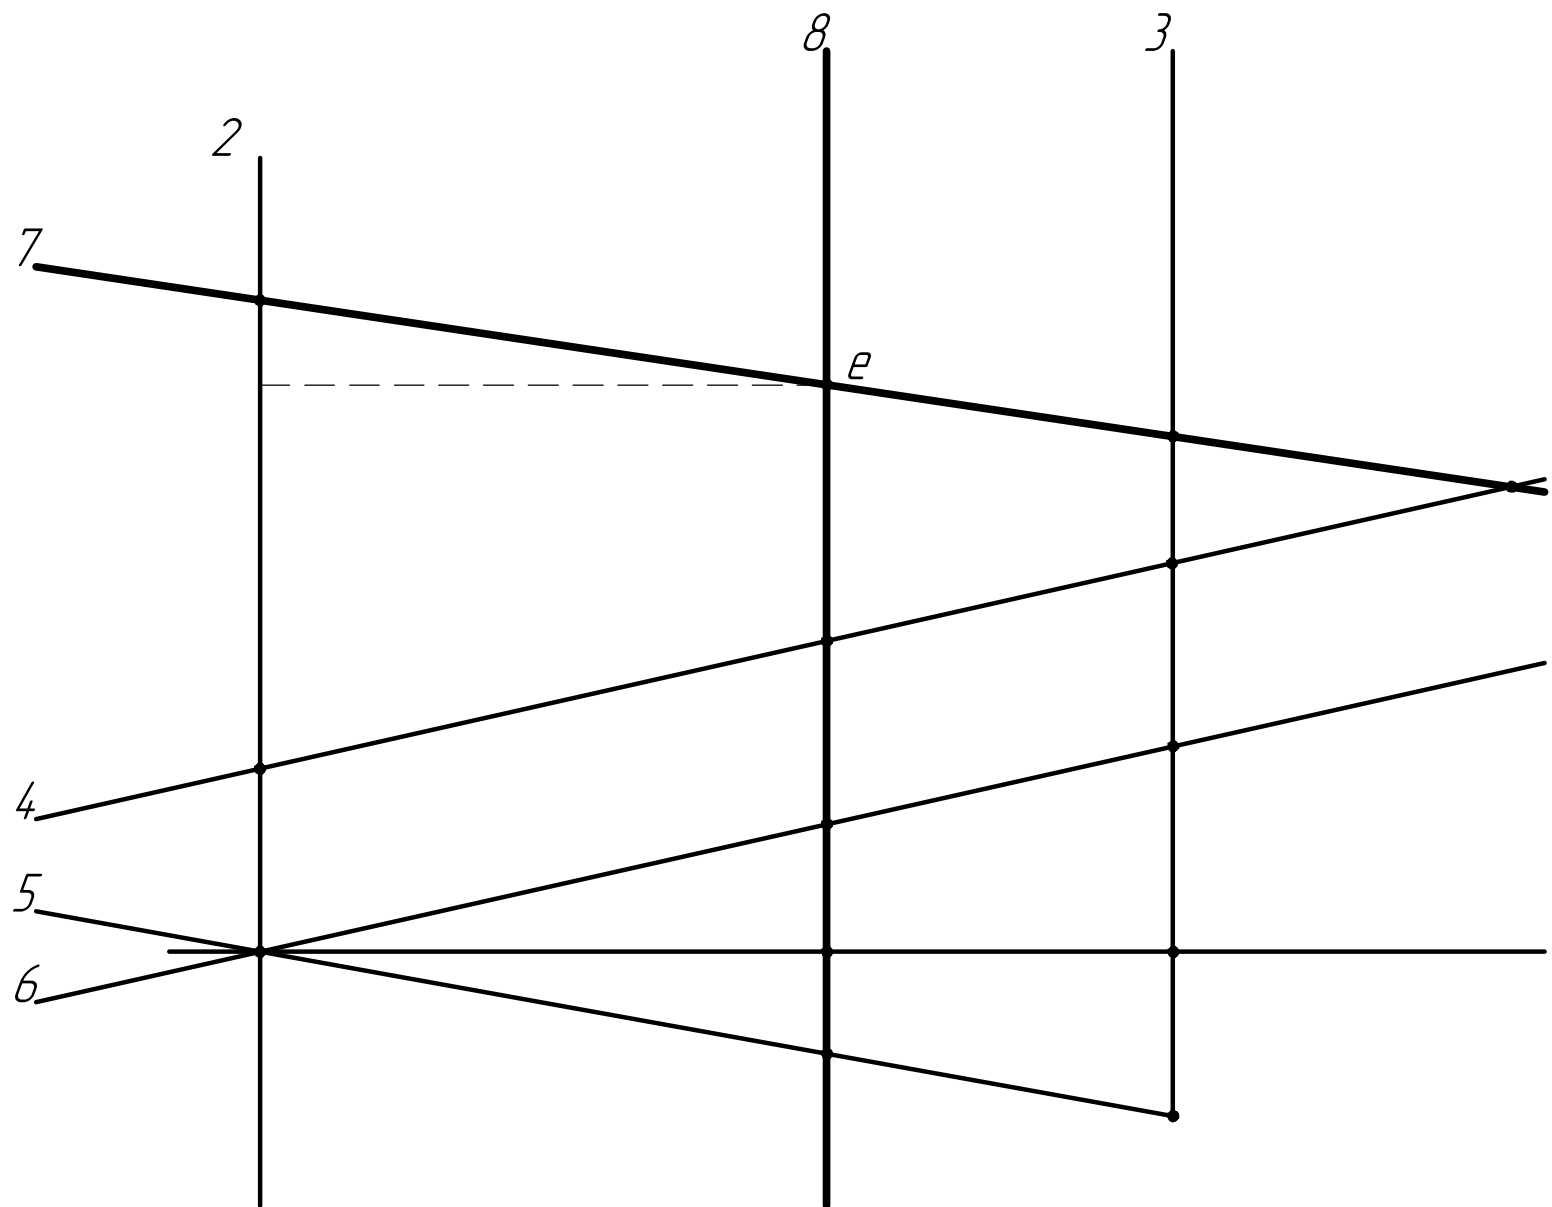




Номер передачи	КПД	i_{ox}	Элементы управления					
			T2	T3	T4	T5	M7	M8
3X II	0,940	-3,459		X		X		
3X I	0,951	-5,568				X		X
I	0,969	4,606			X	X		
II	0,980	2,048	X		X			
III	0,989	14,03			X			X
IV	0,981	1,177		X	X			
V	0,994	1,146			X		X	
VI	0,991	1,123		X			X	
VII	1,000	1,000					X	X
VIII	0,992	0,948	X				X	

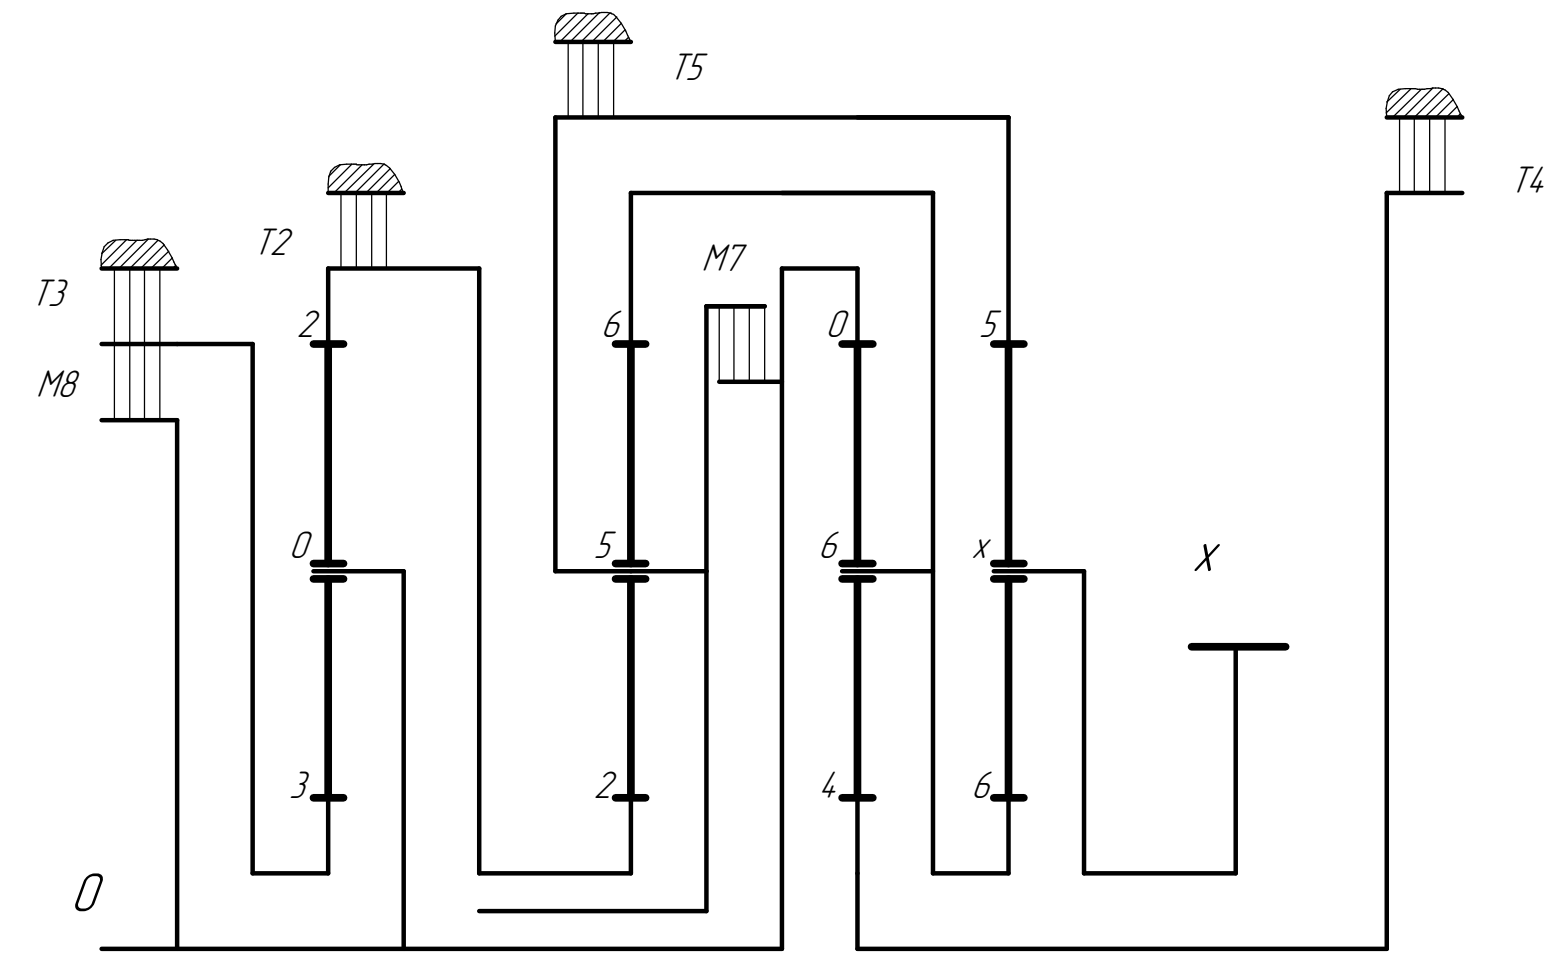

КПСМ 09.2026.05.000 СБ				Планетарная каретка передач		
Изм.	Лист	№ докум.	Подп.	Дата	Изм.	Лист
Разраб.	Жилкина Н.Д.	4,02				12
Проф.	Лавренко С.А.					
Т.контр.						
Н.контр.						
Изд.						


Копировал

Формат А1


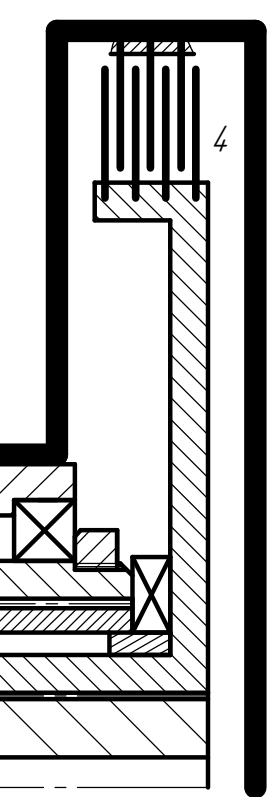
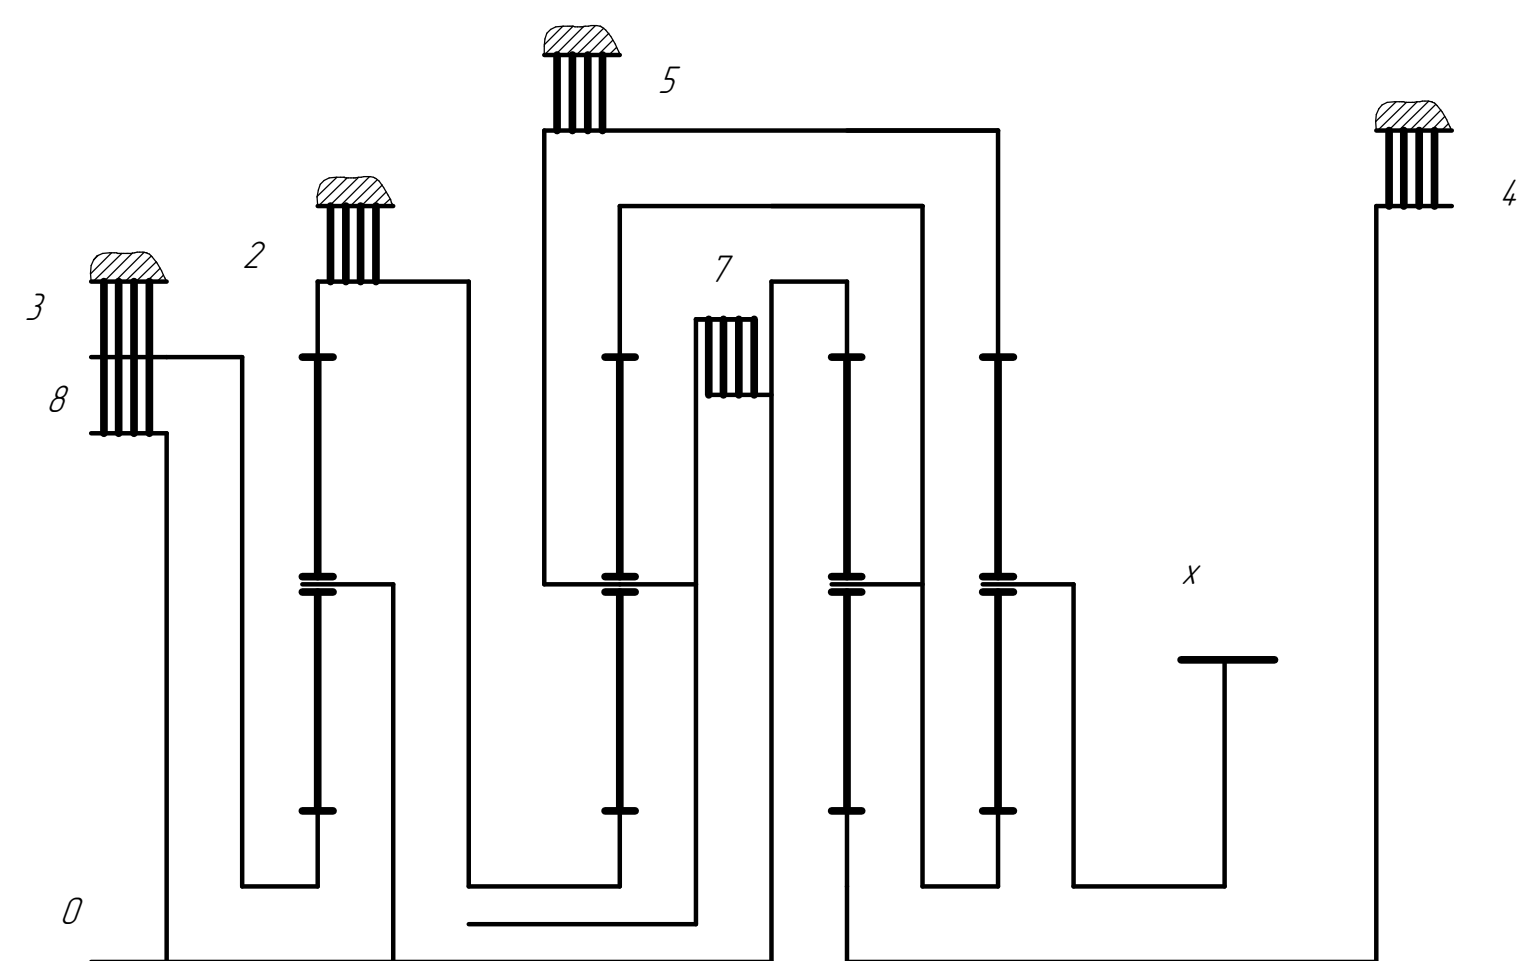
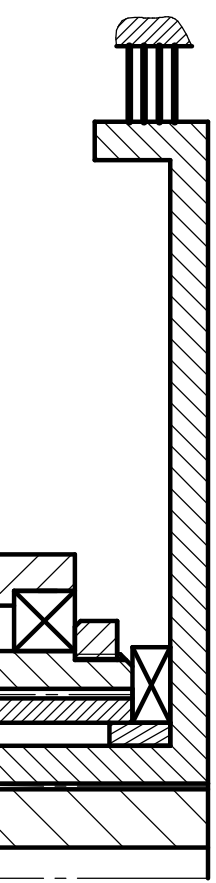


КПМ 09.2026.05.000 СБ

Б A-A B Г Д

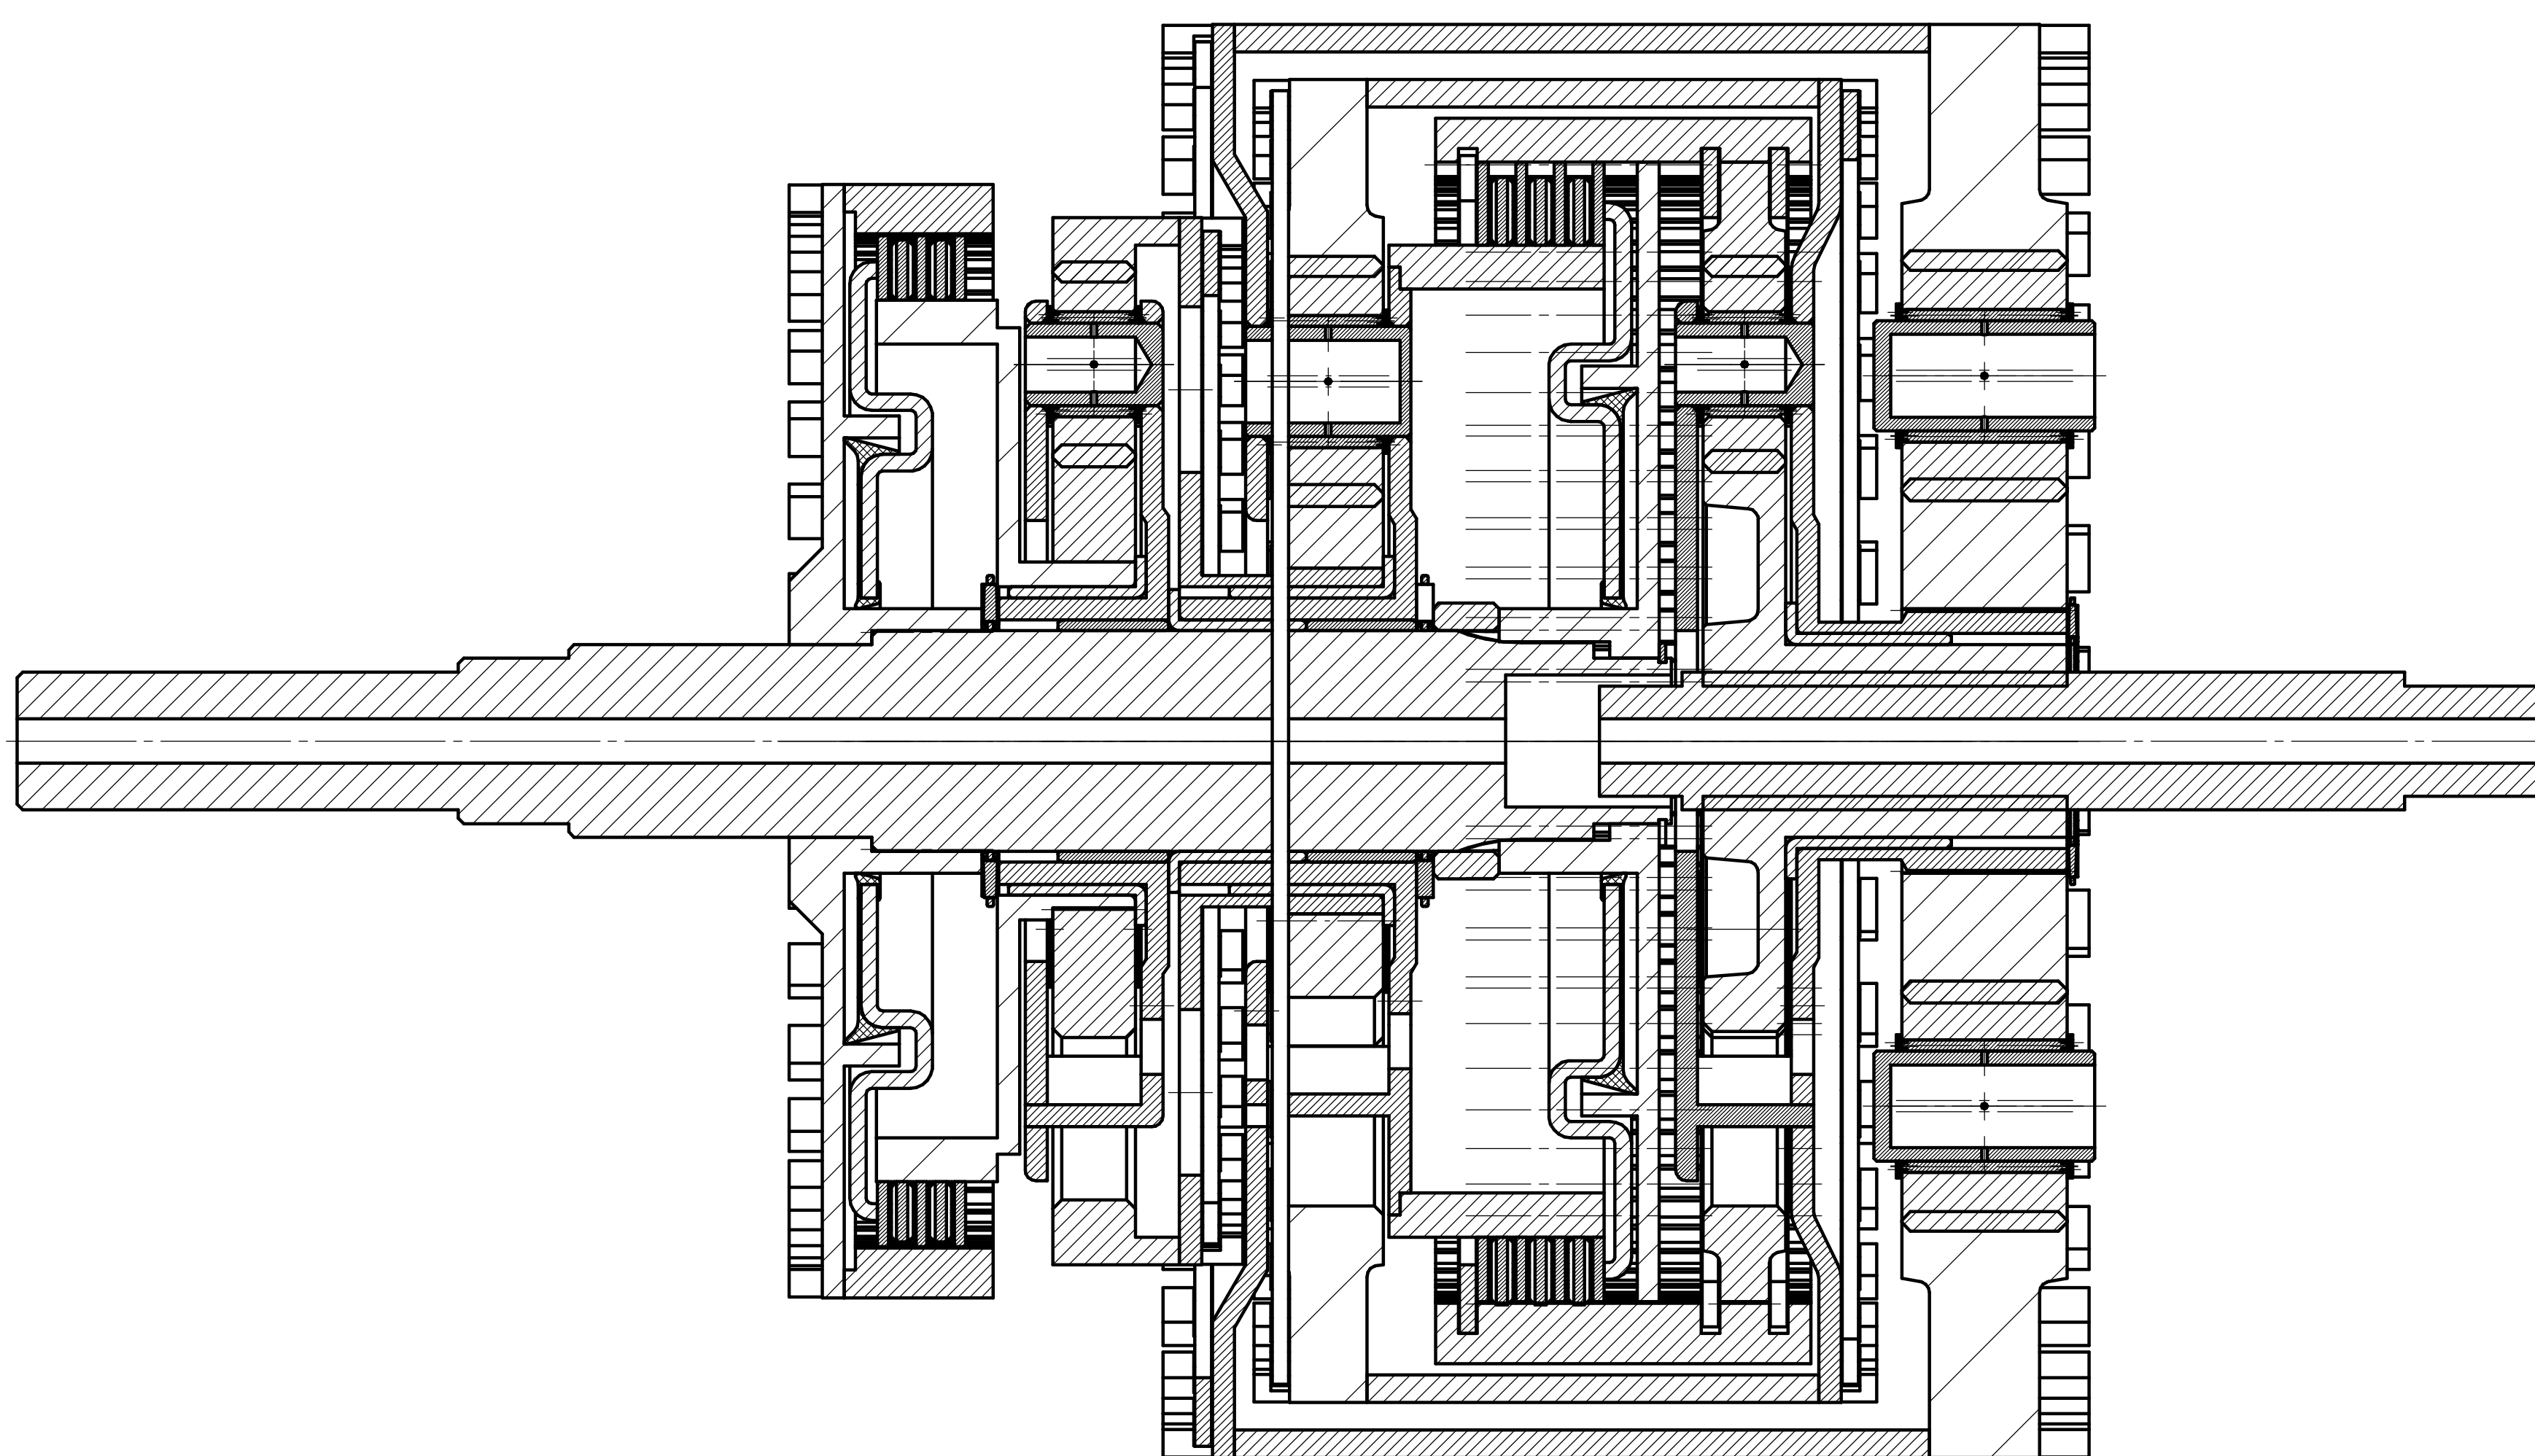

Б B Г Д

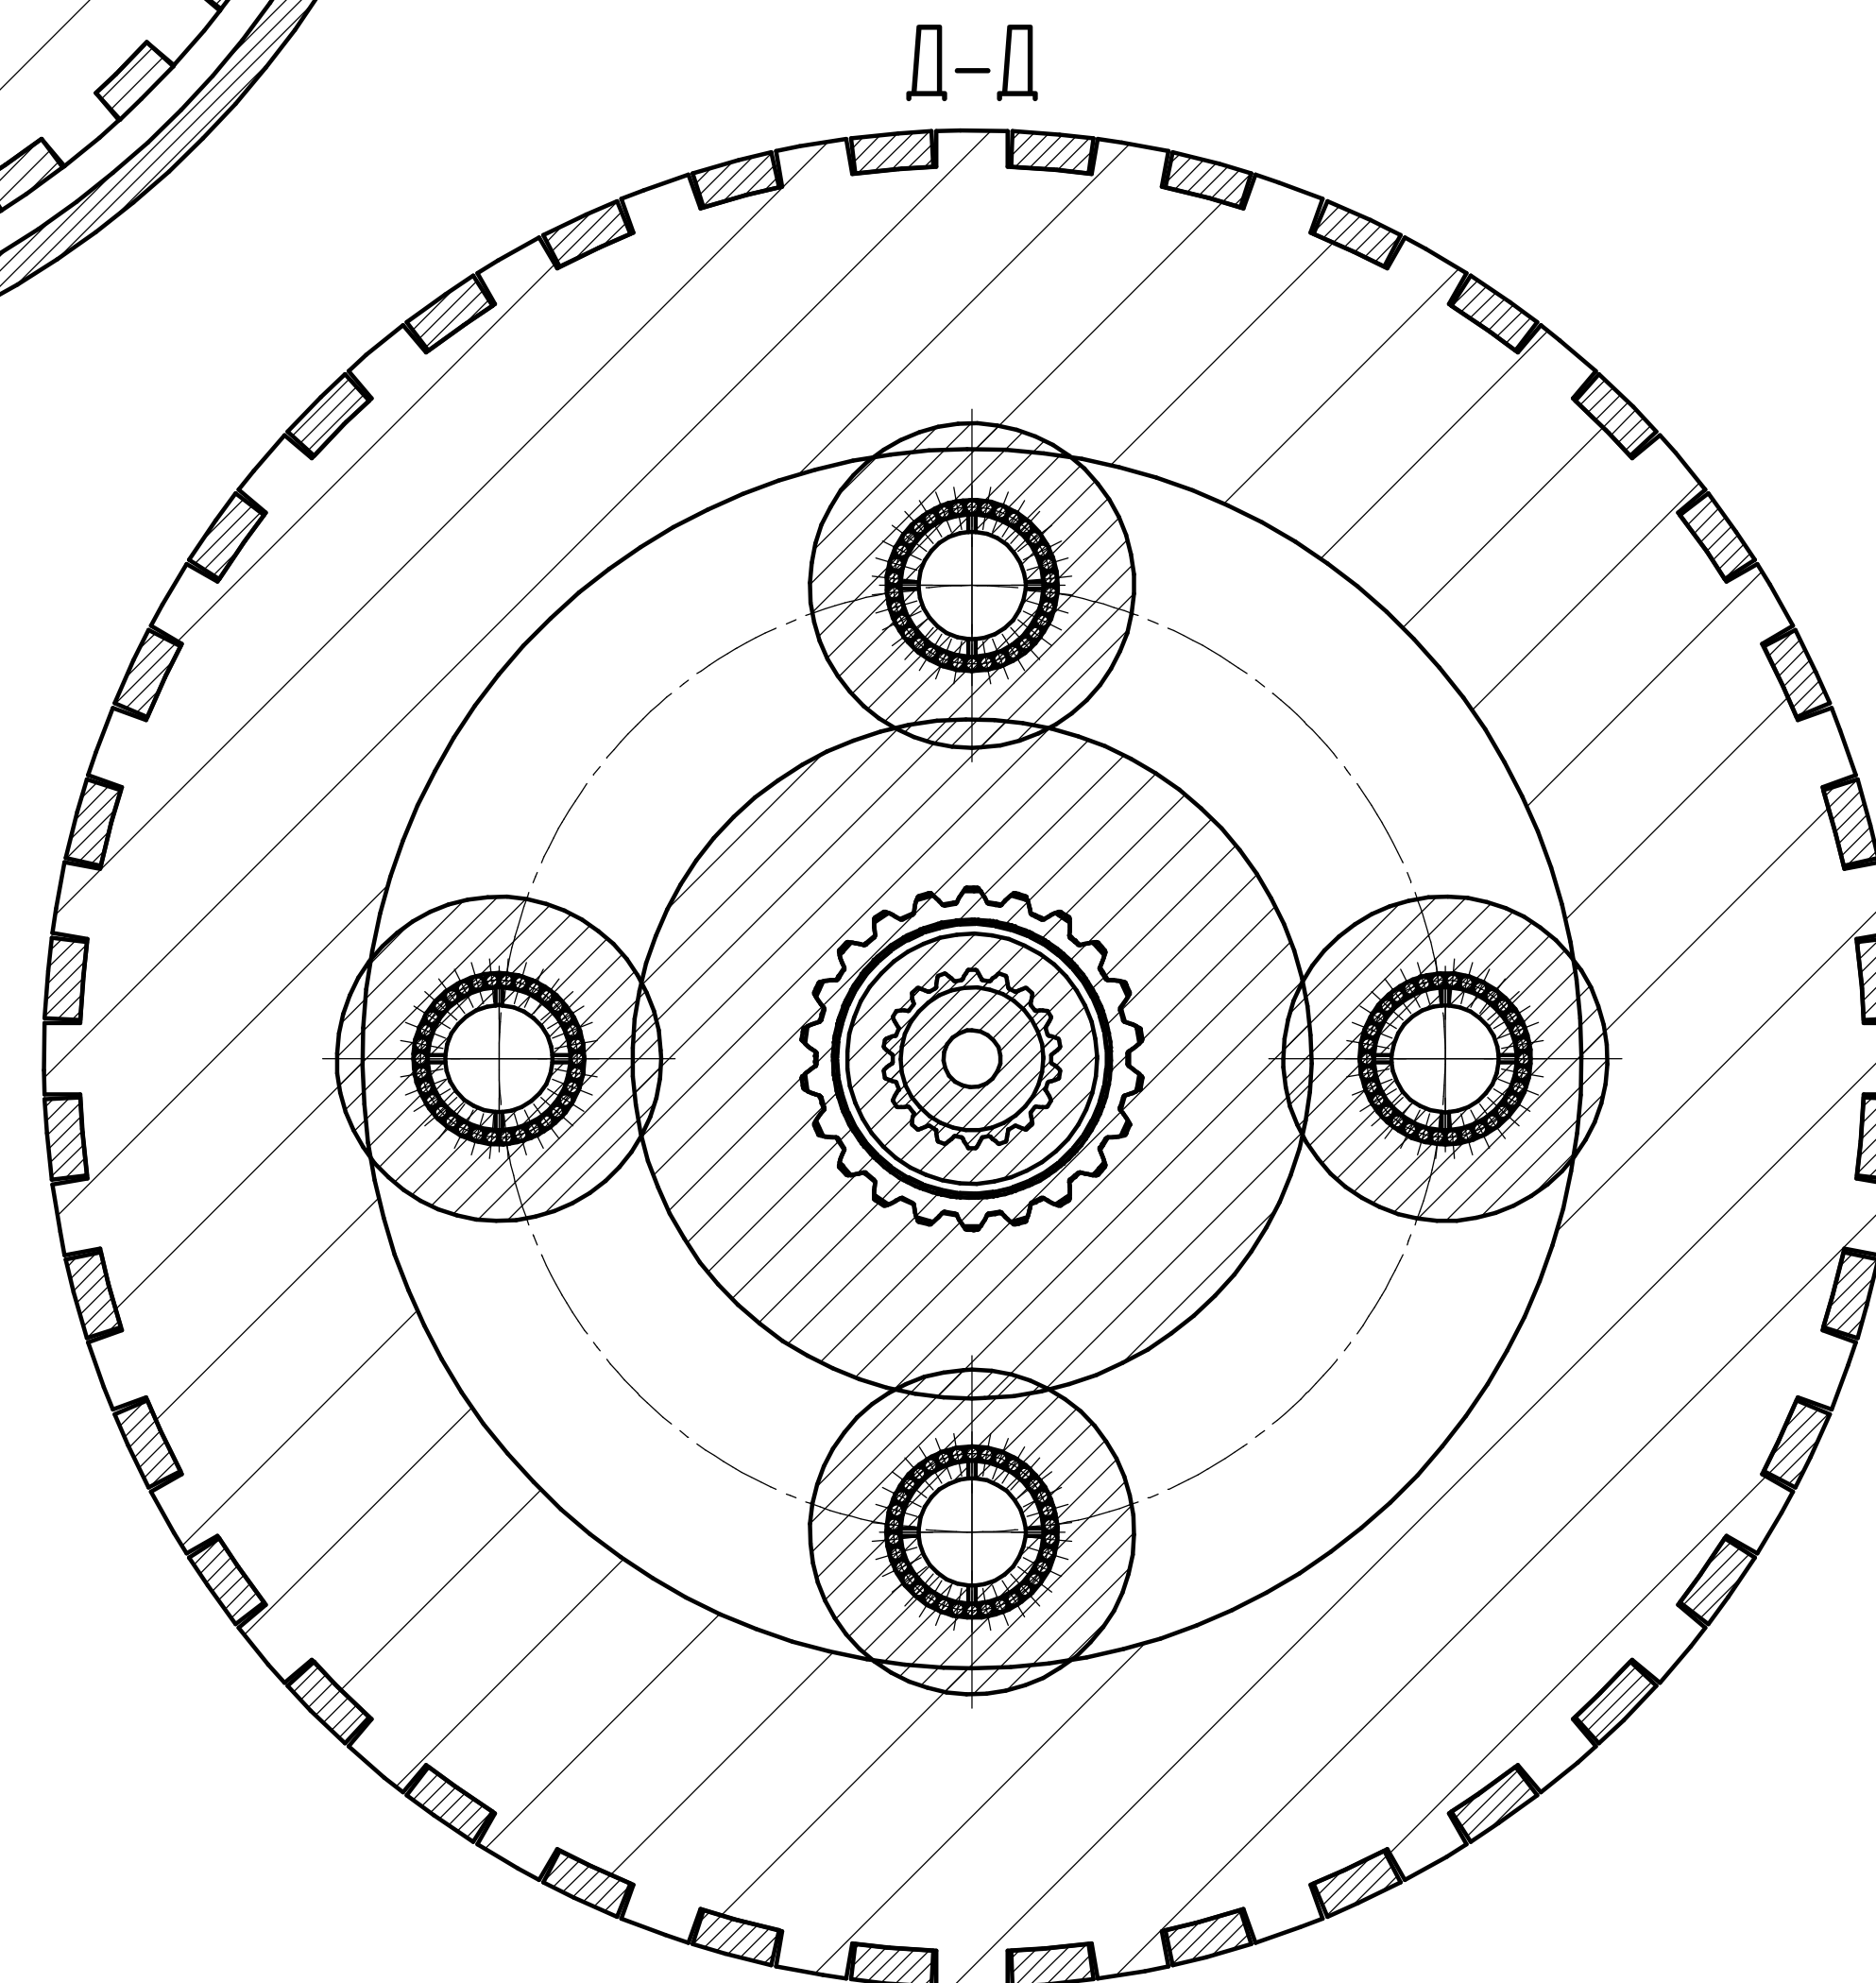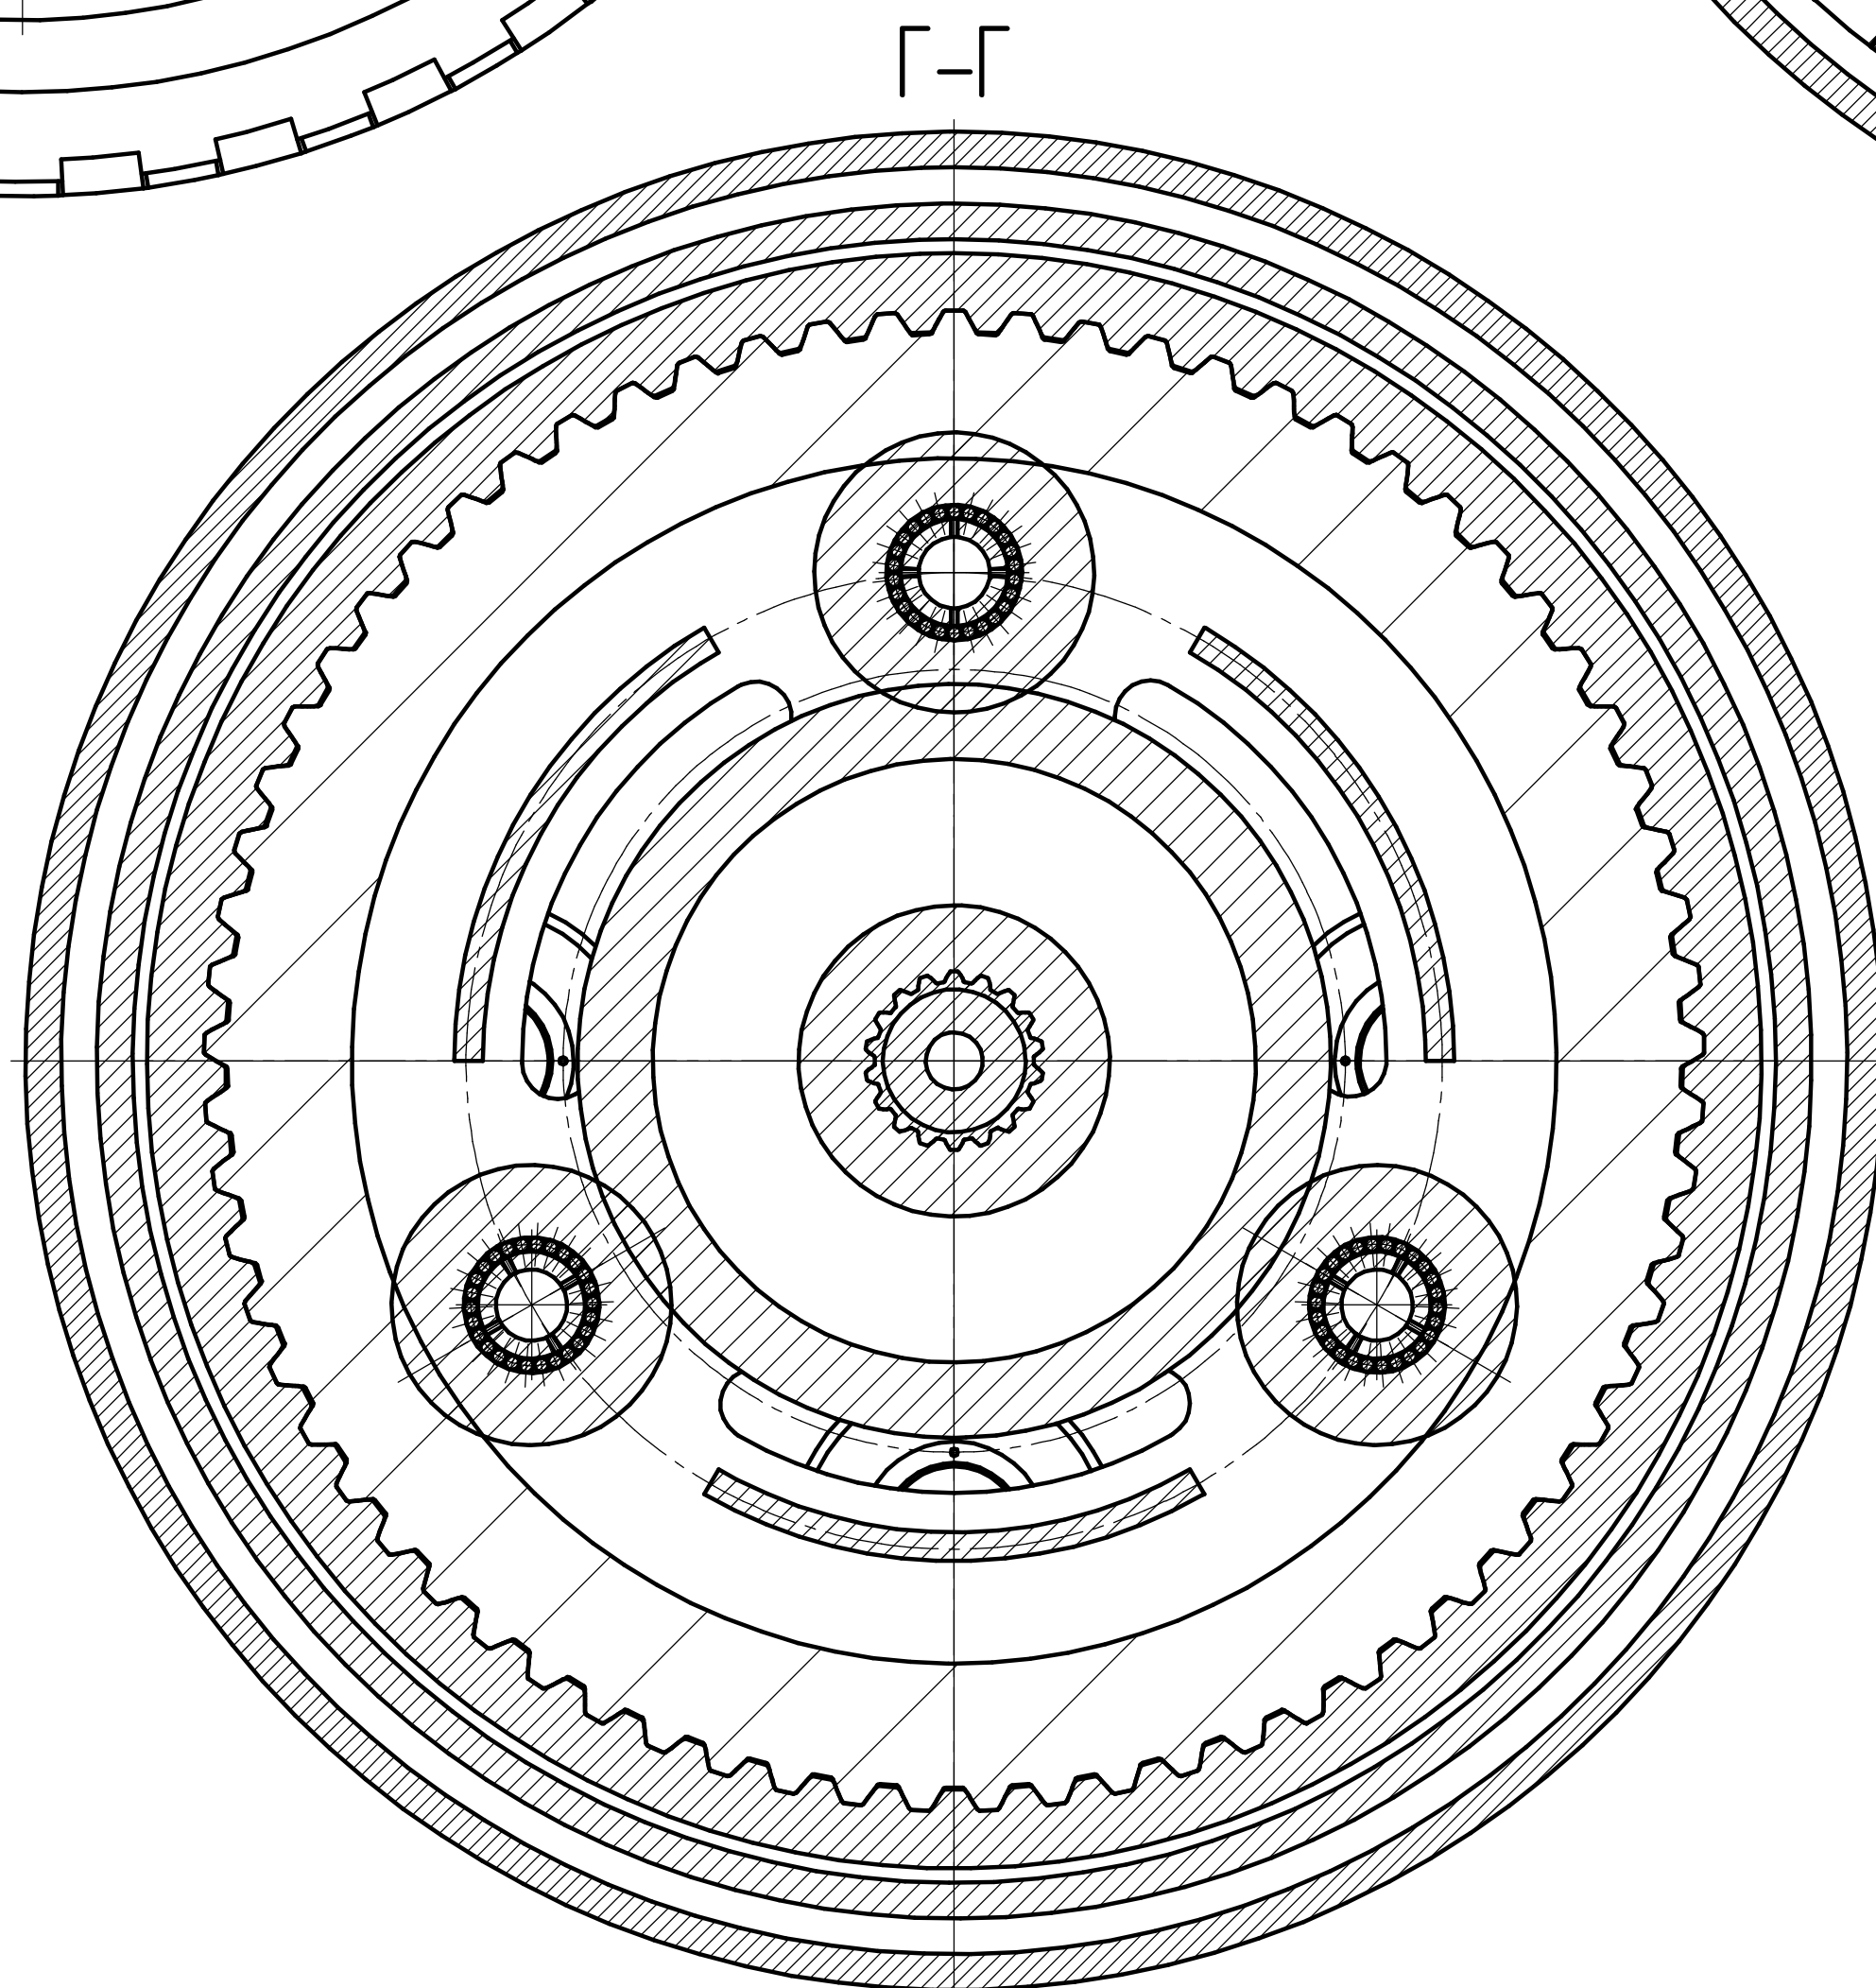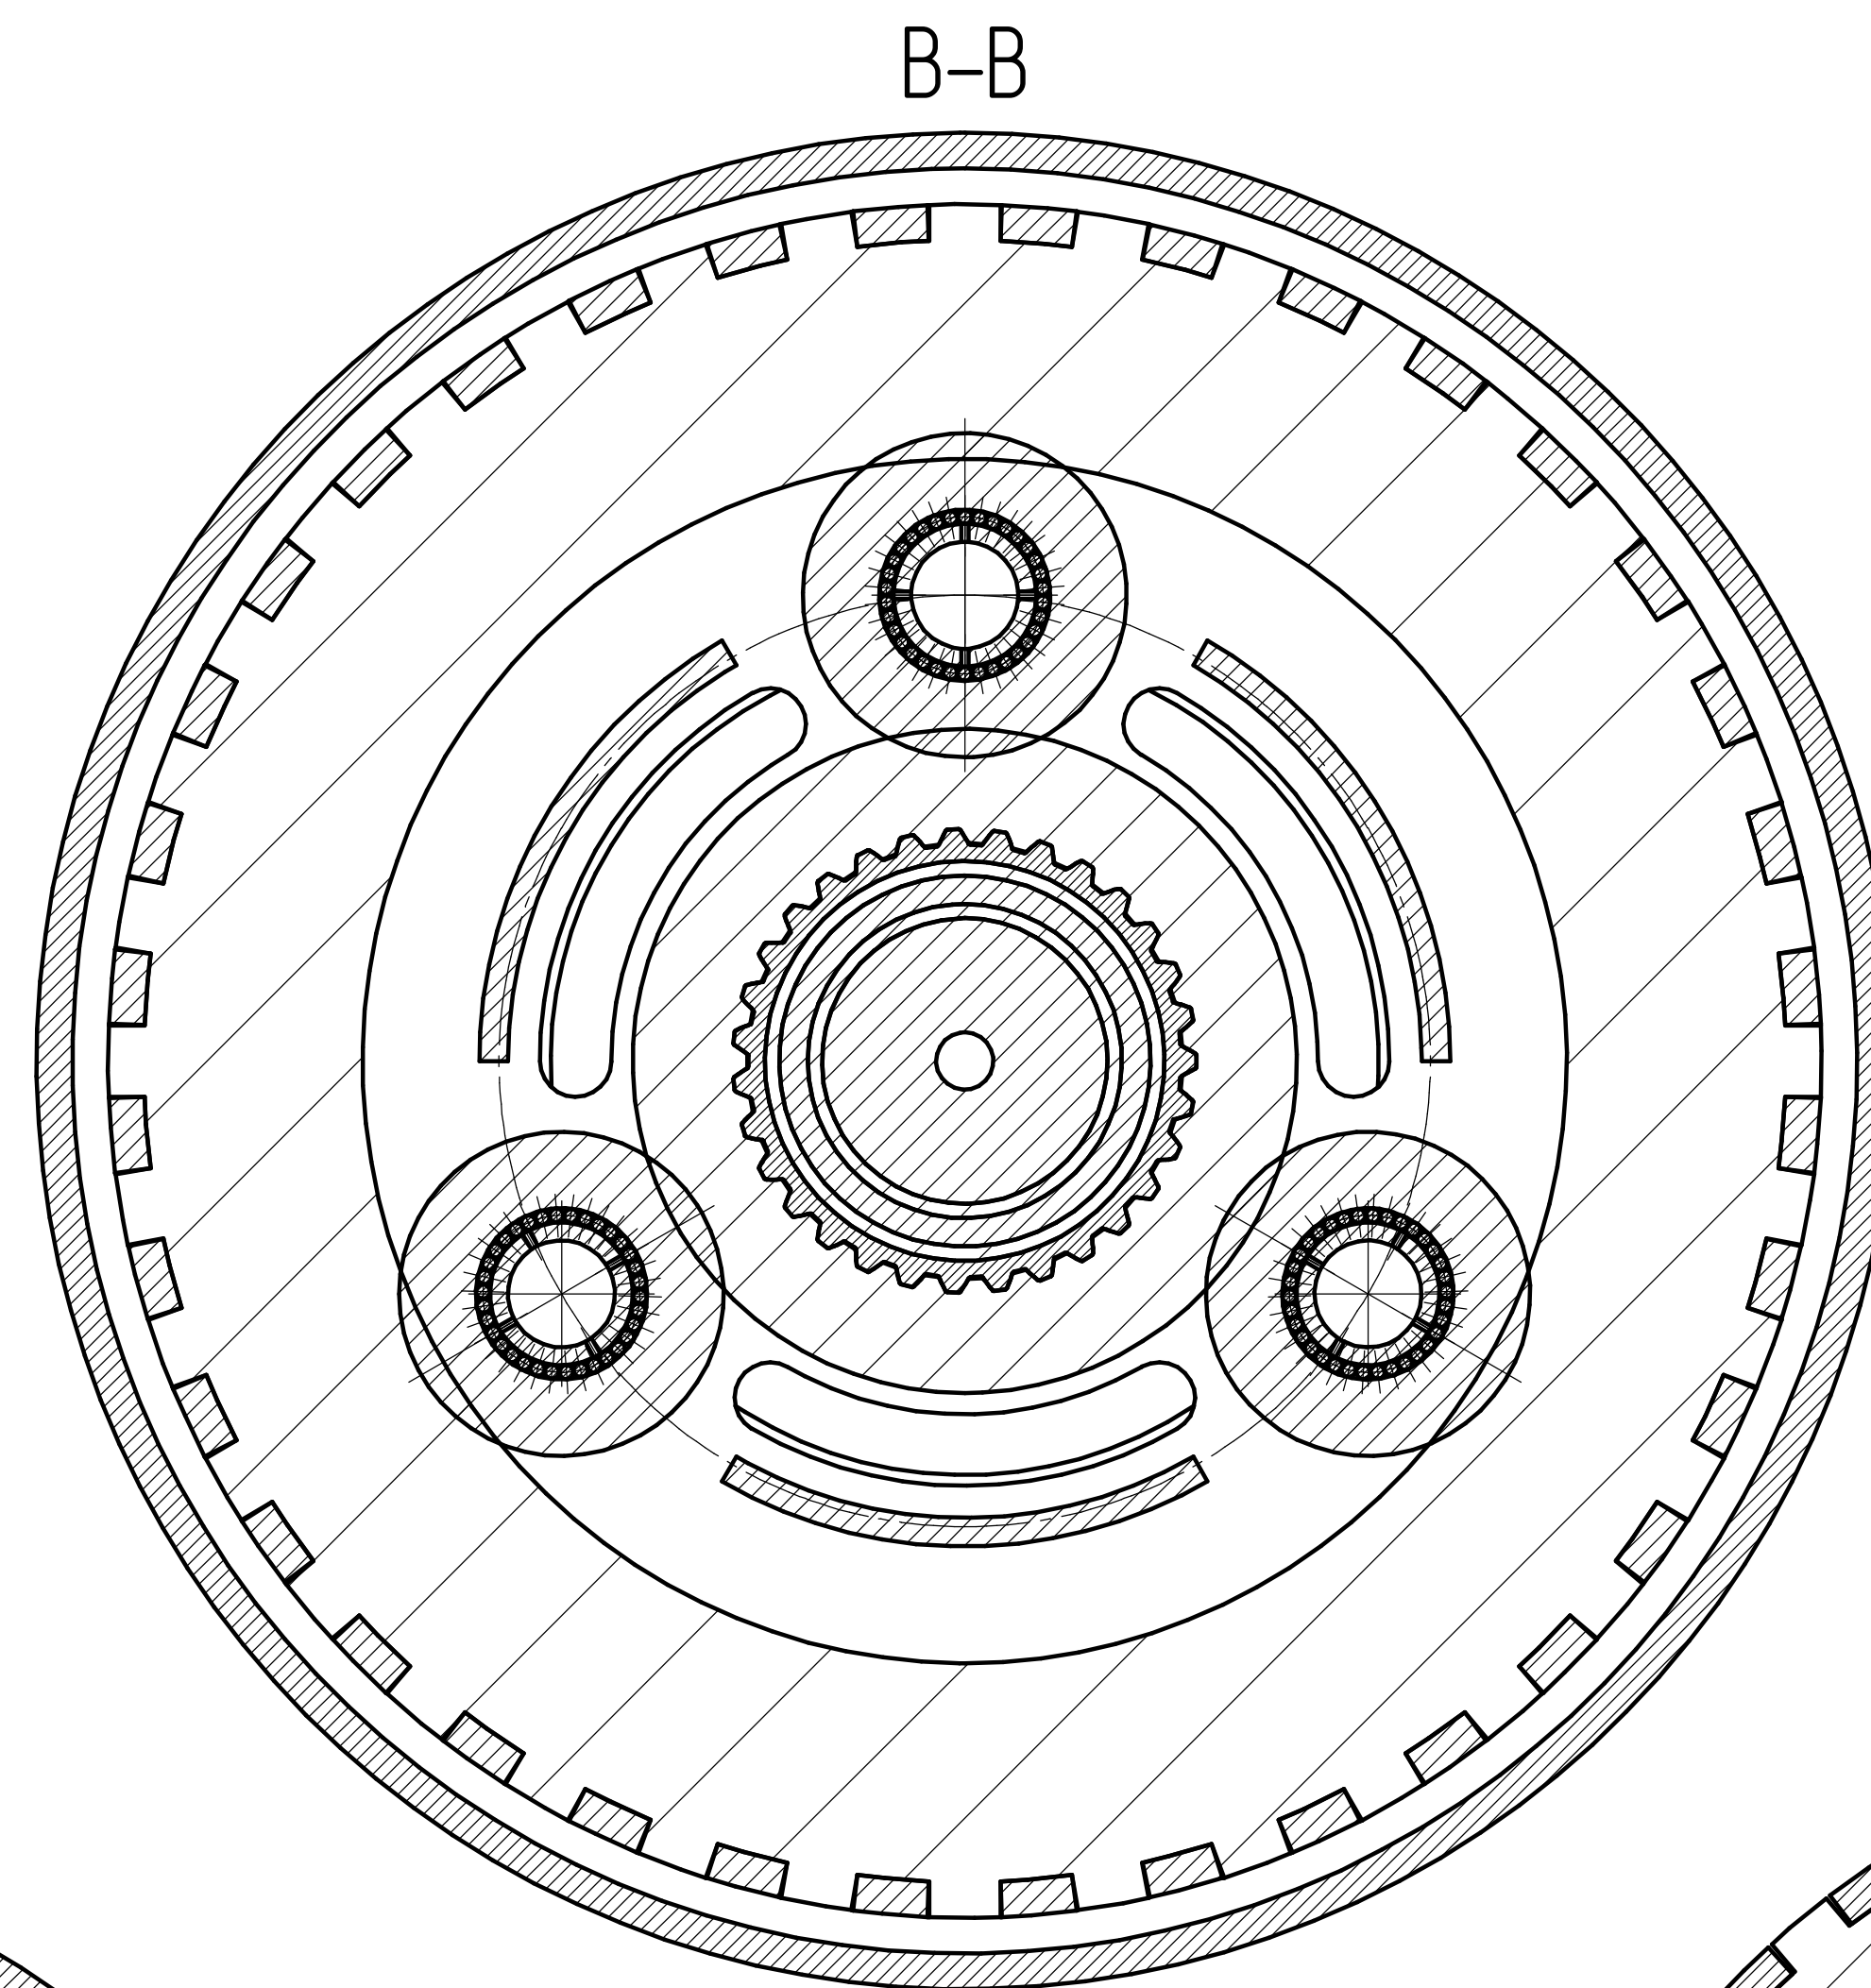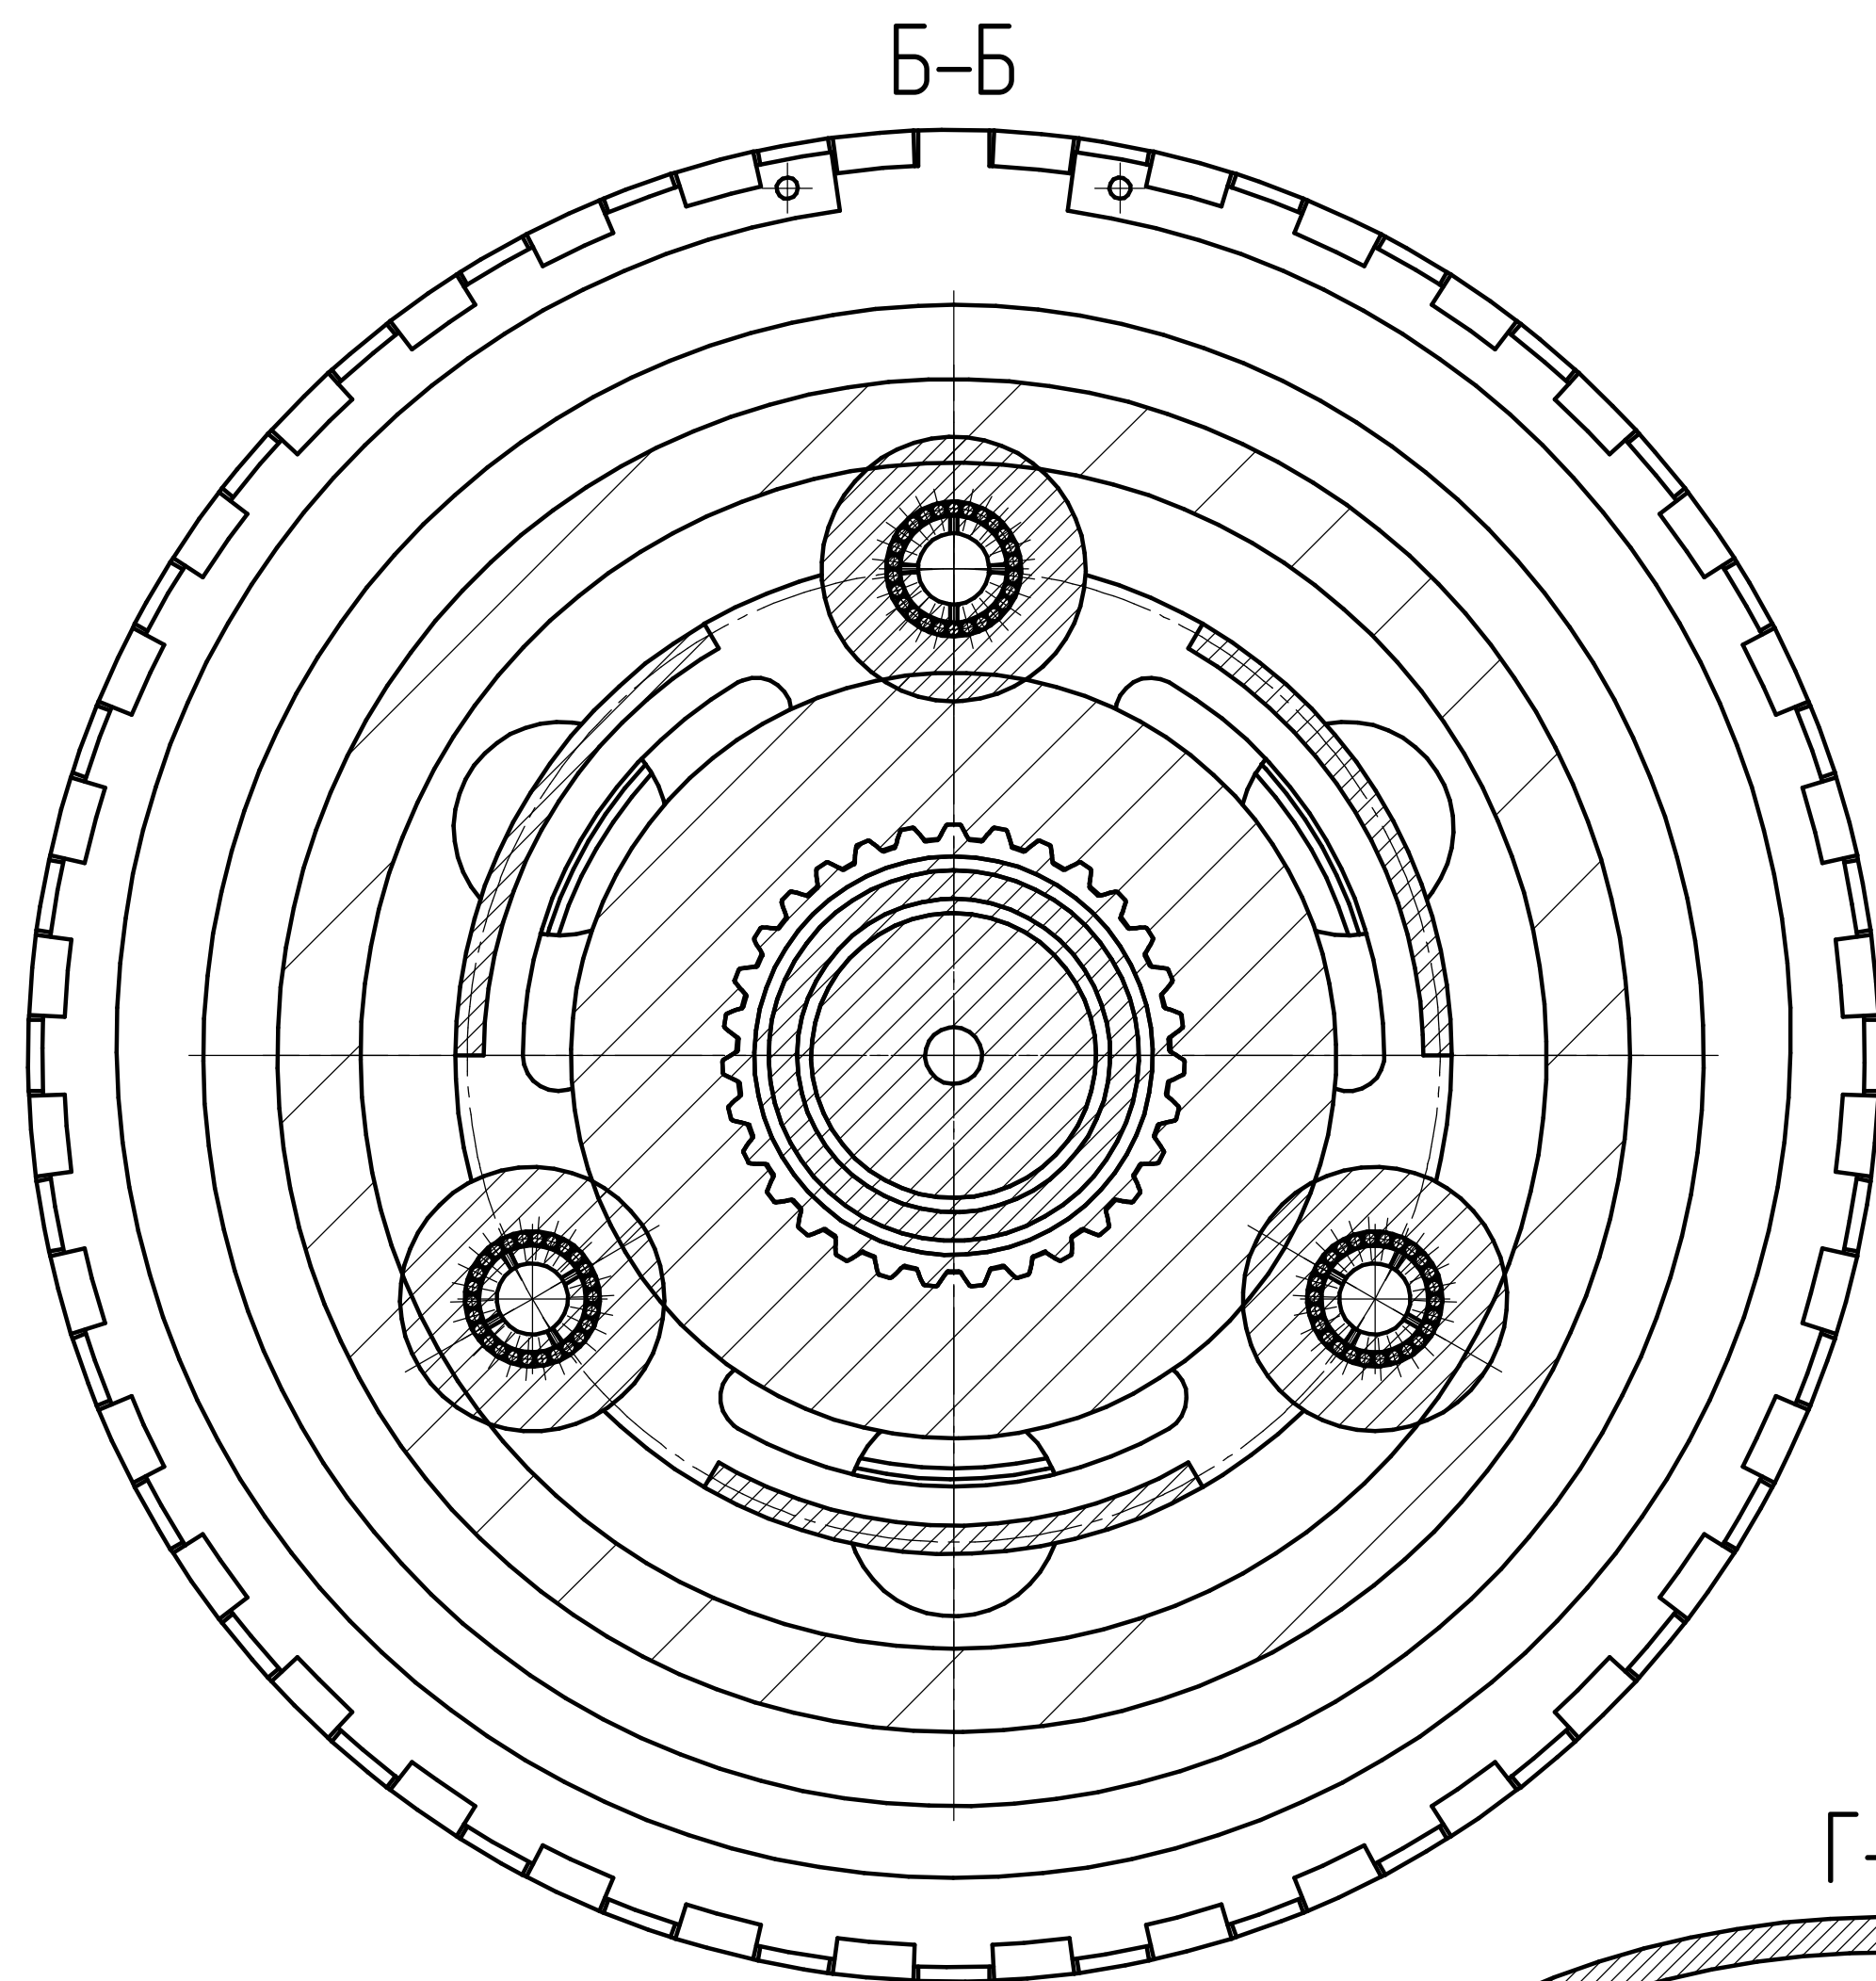

КПСМ 09.2026.05.000 СБ

КМПУС-ЭП 123 Учредителю © 2024 ООО "АНО-Служба проектных". Разрешено копировать, распространять, публиковать, использовать в коммерческих целях. Все права защищены.

Имя	№ докум.	Подп.	Имя	№ докум.	Подп.	Имя	№ докум.	Подп.	Имя	№ докум.	Подп.

Имя	№ докум.	Подп.	Имя	№ докум.	Подп.	Имя	№ докум.	Подп.	Имя	№ докум.	Подп.

КПСМ 09.2026.05.000 СБ	Лист
	4