
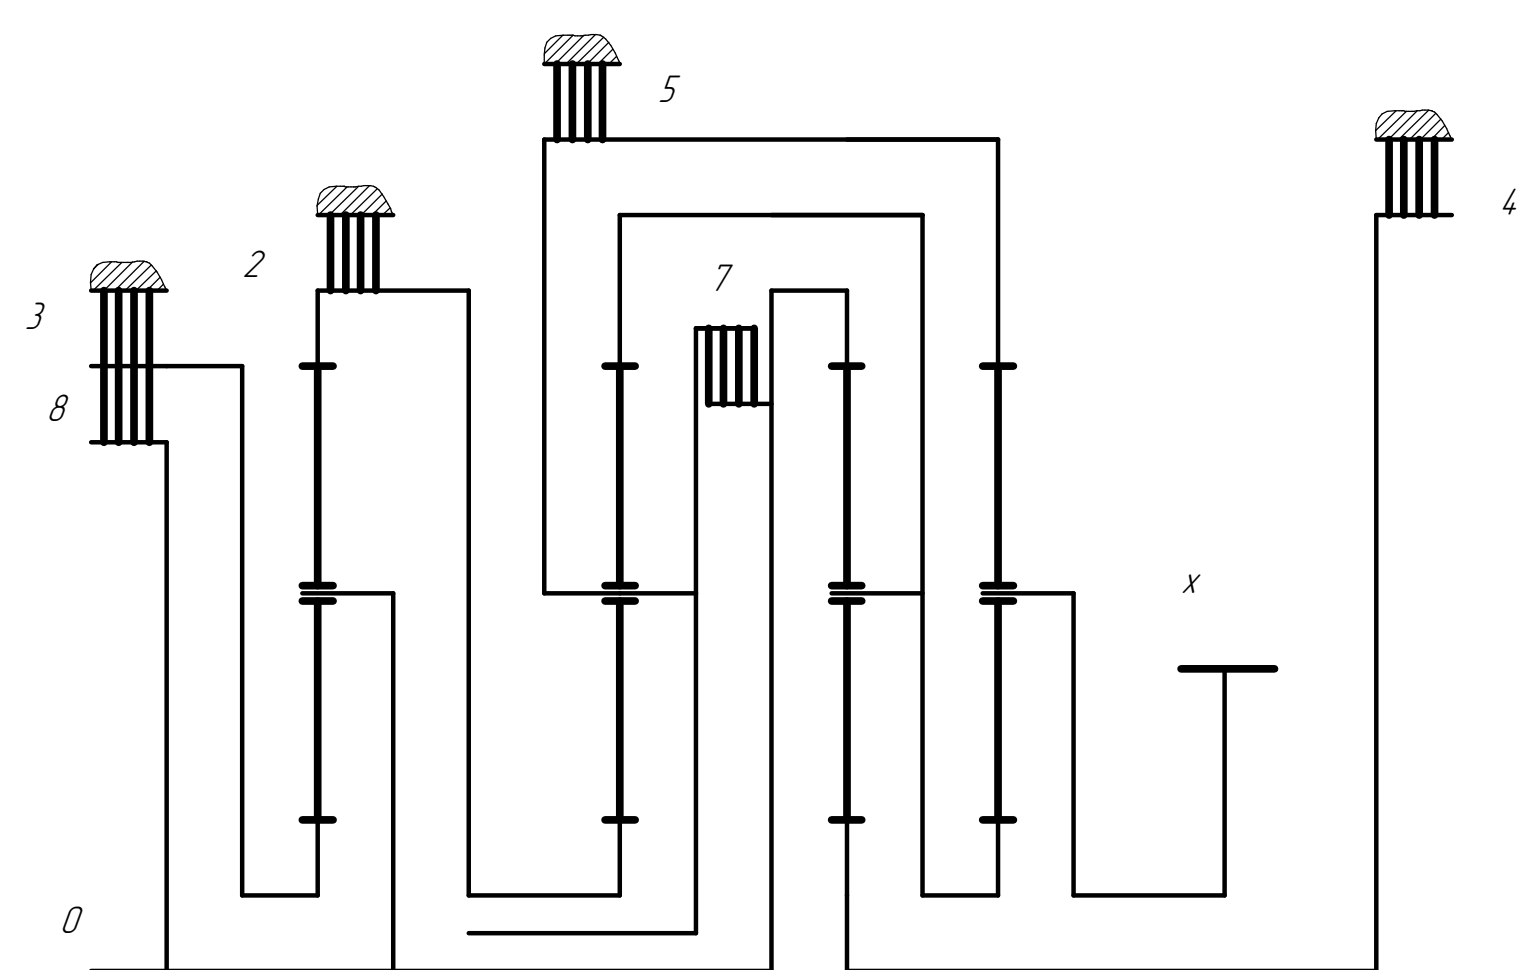
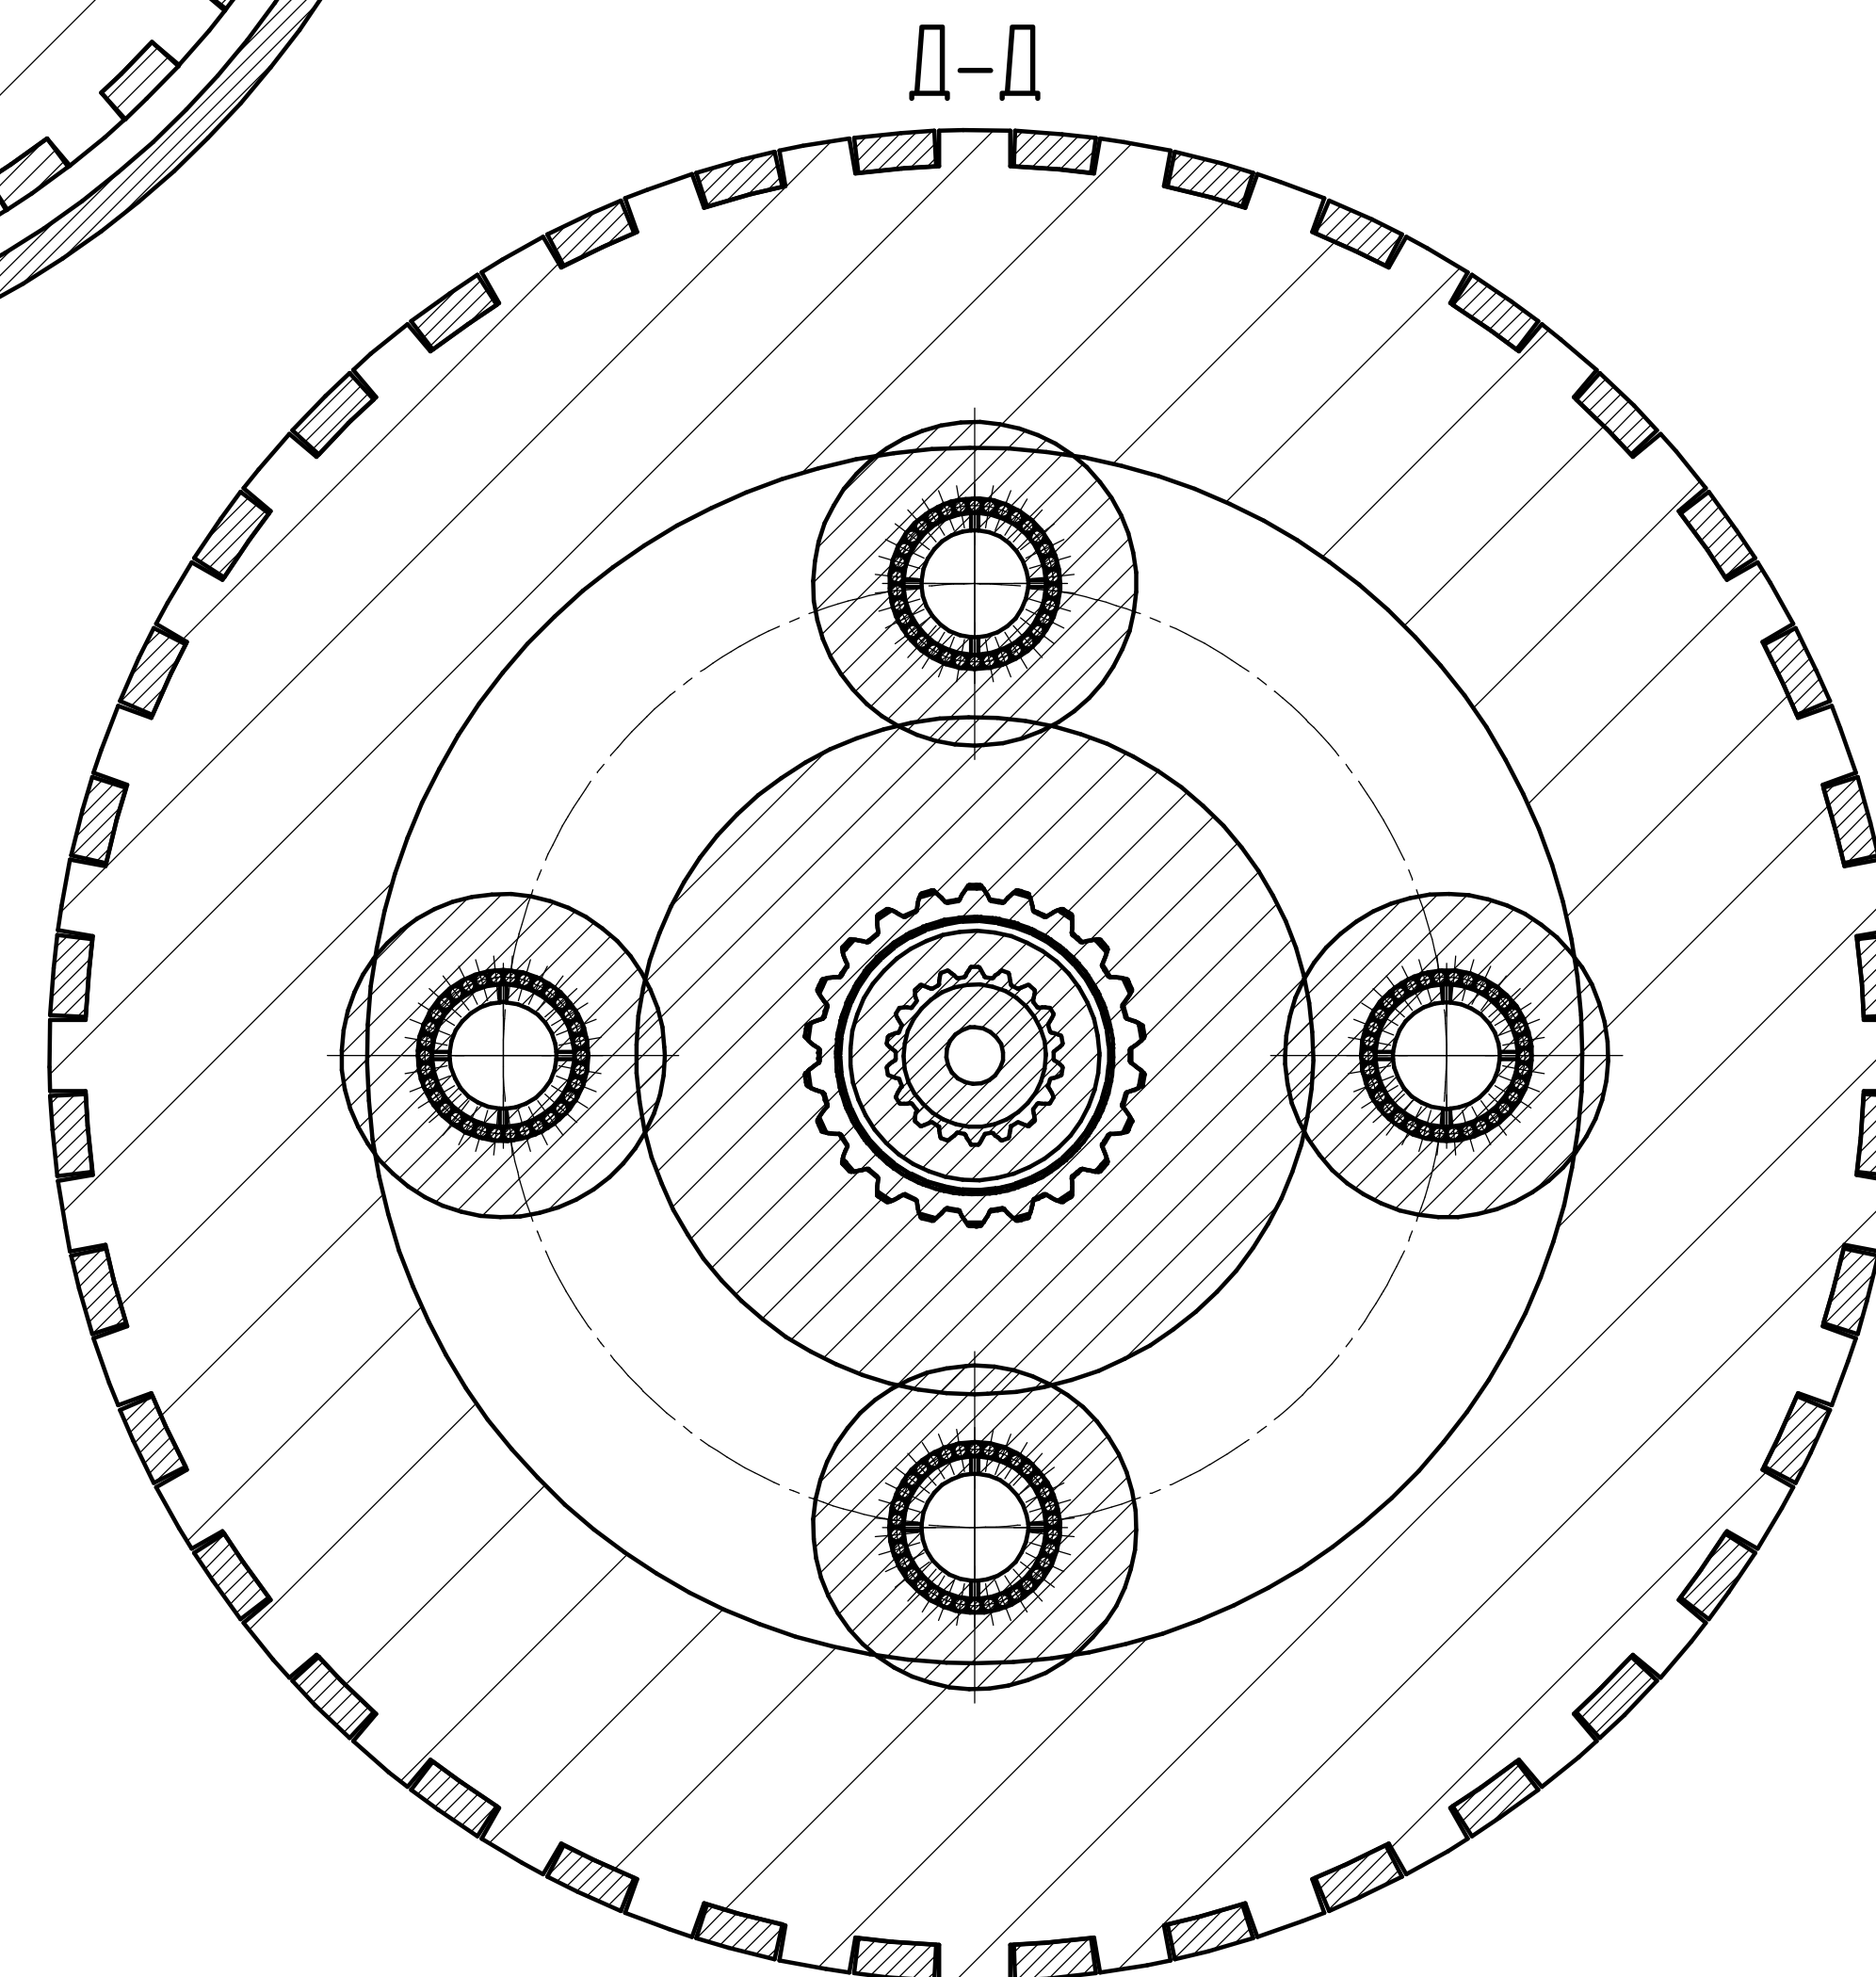
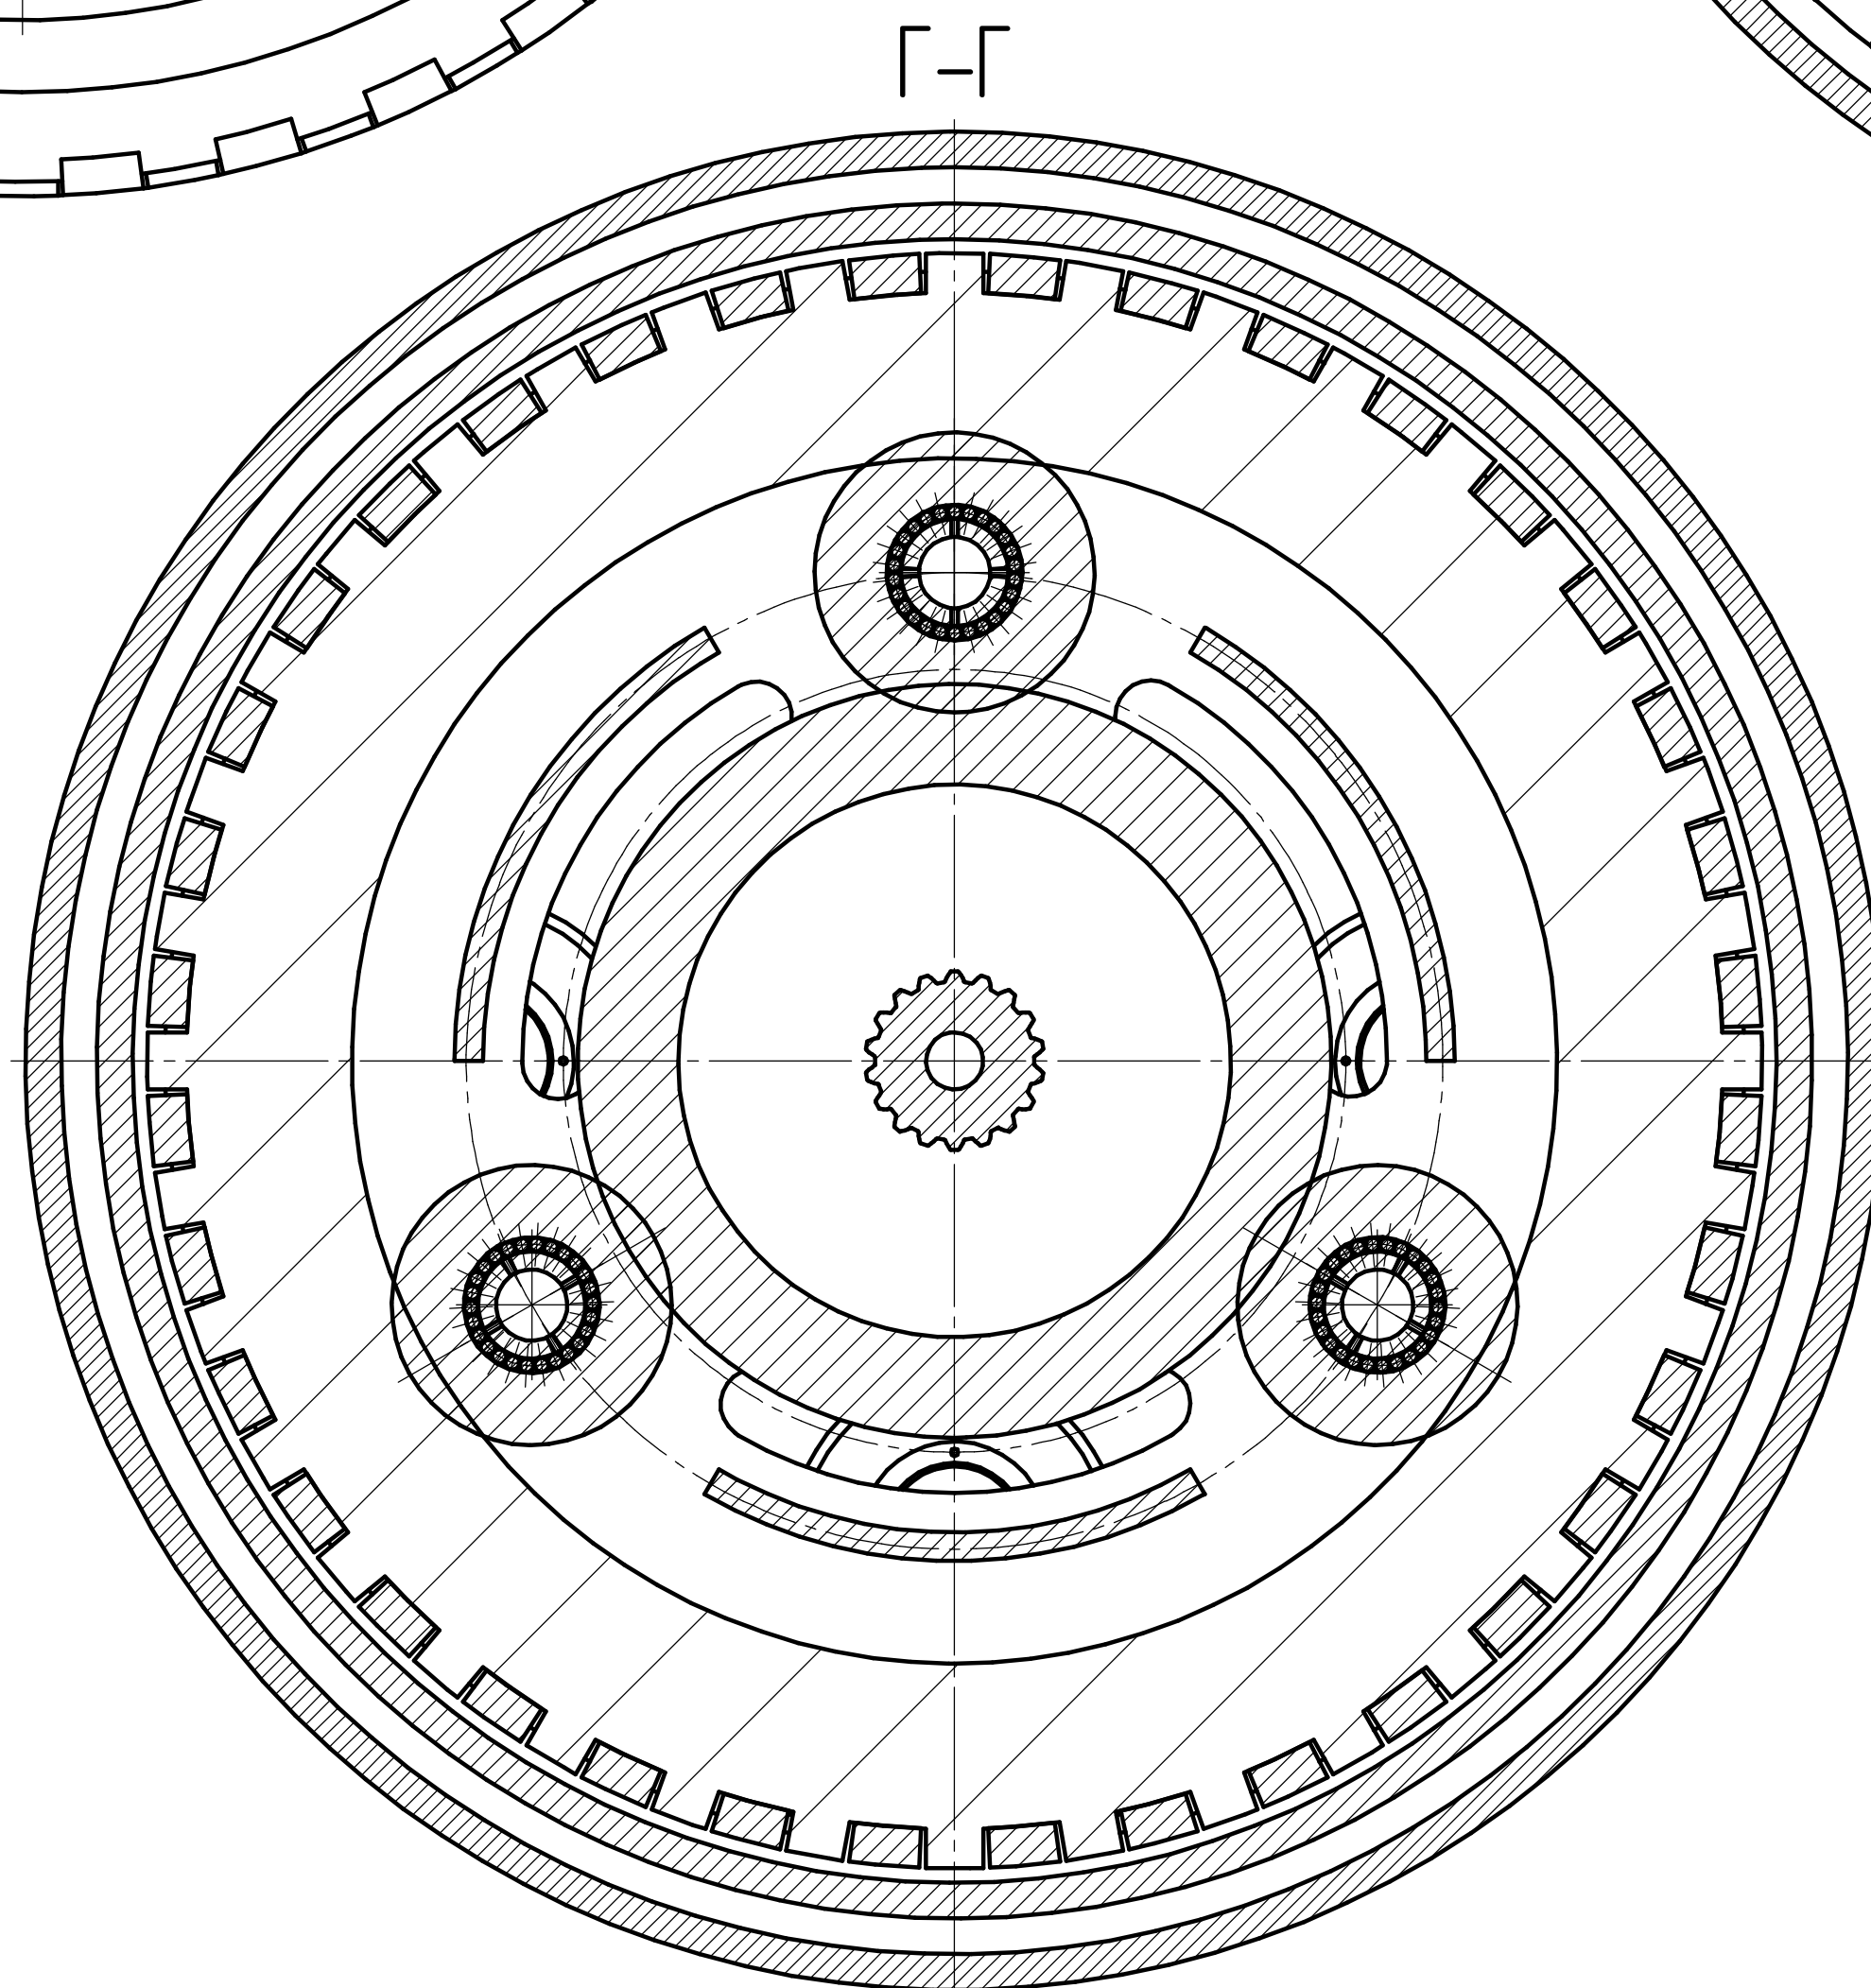
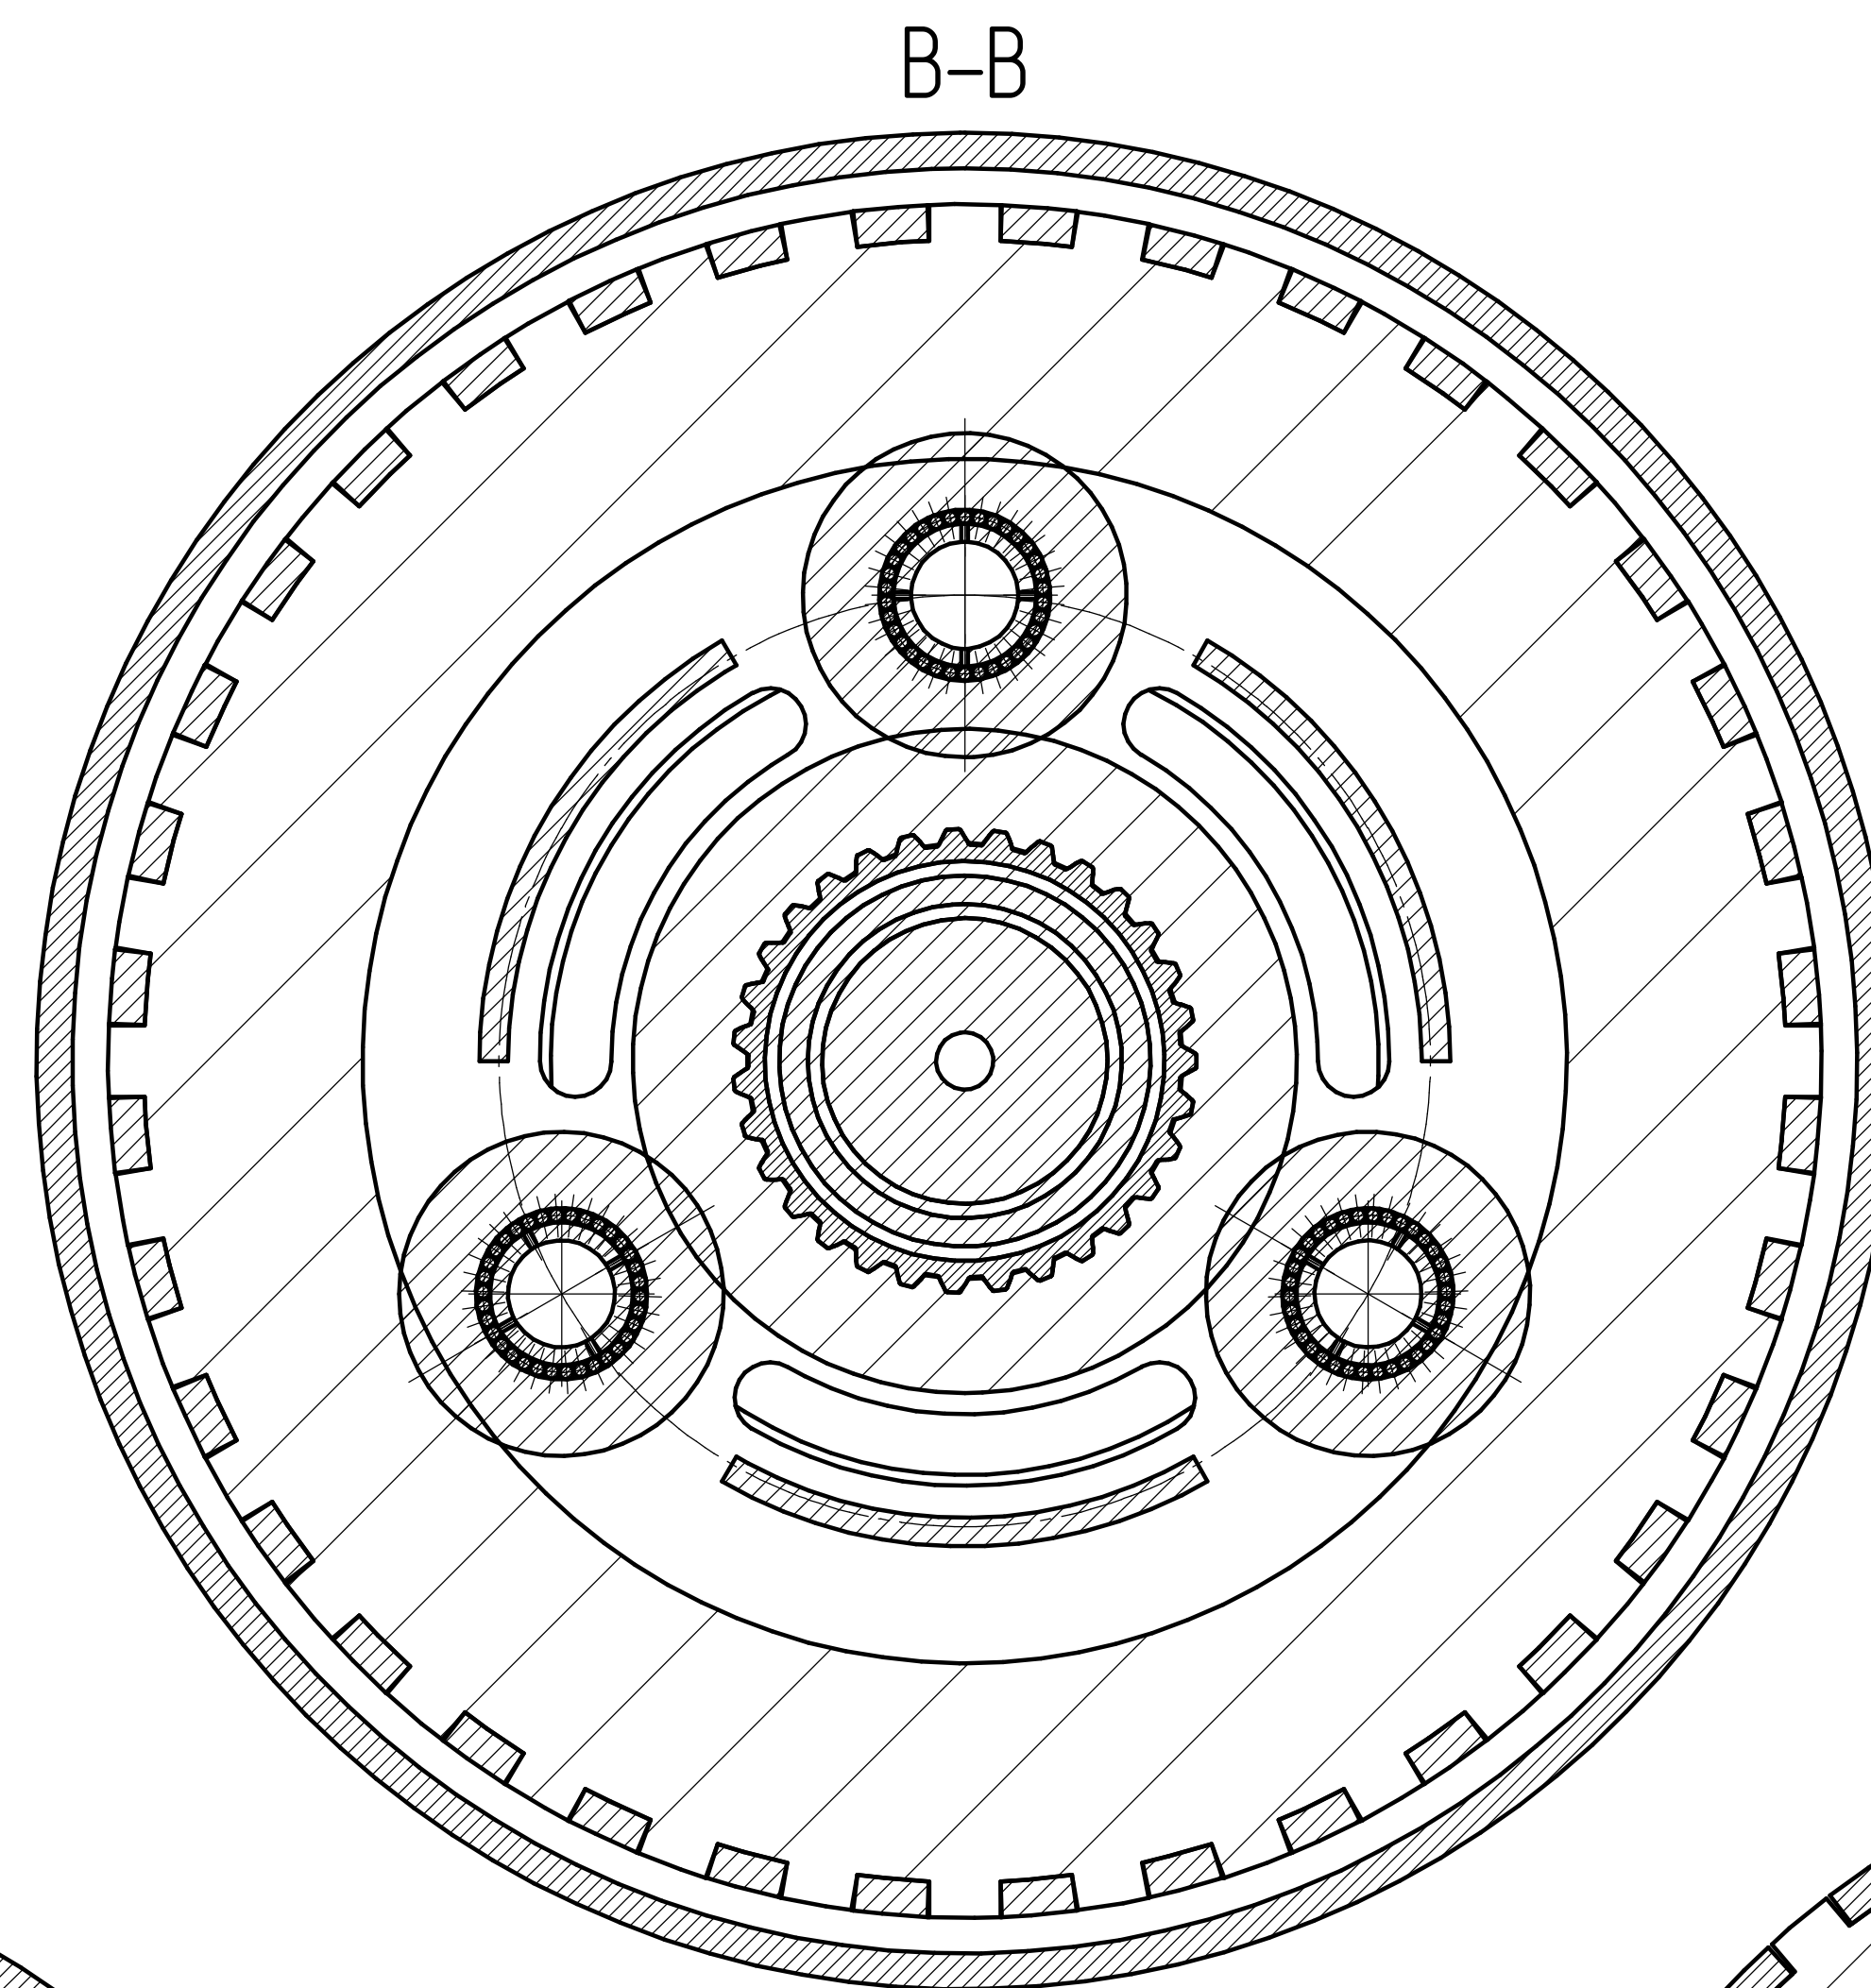


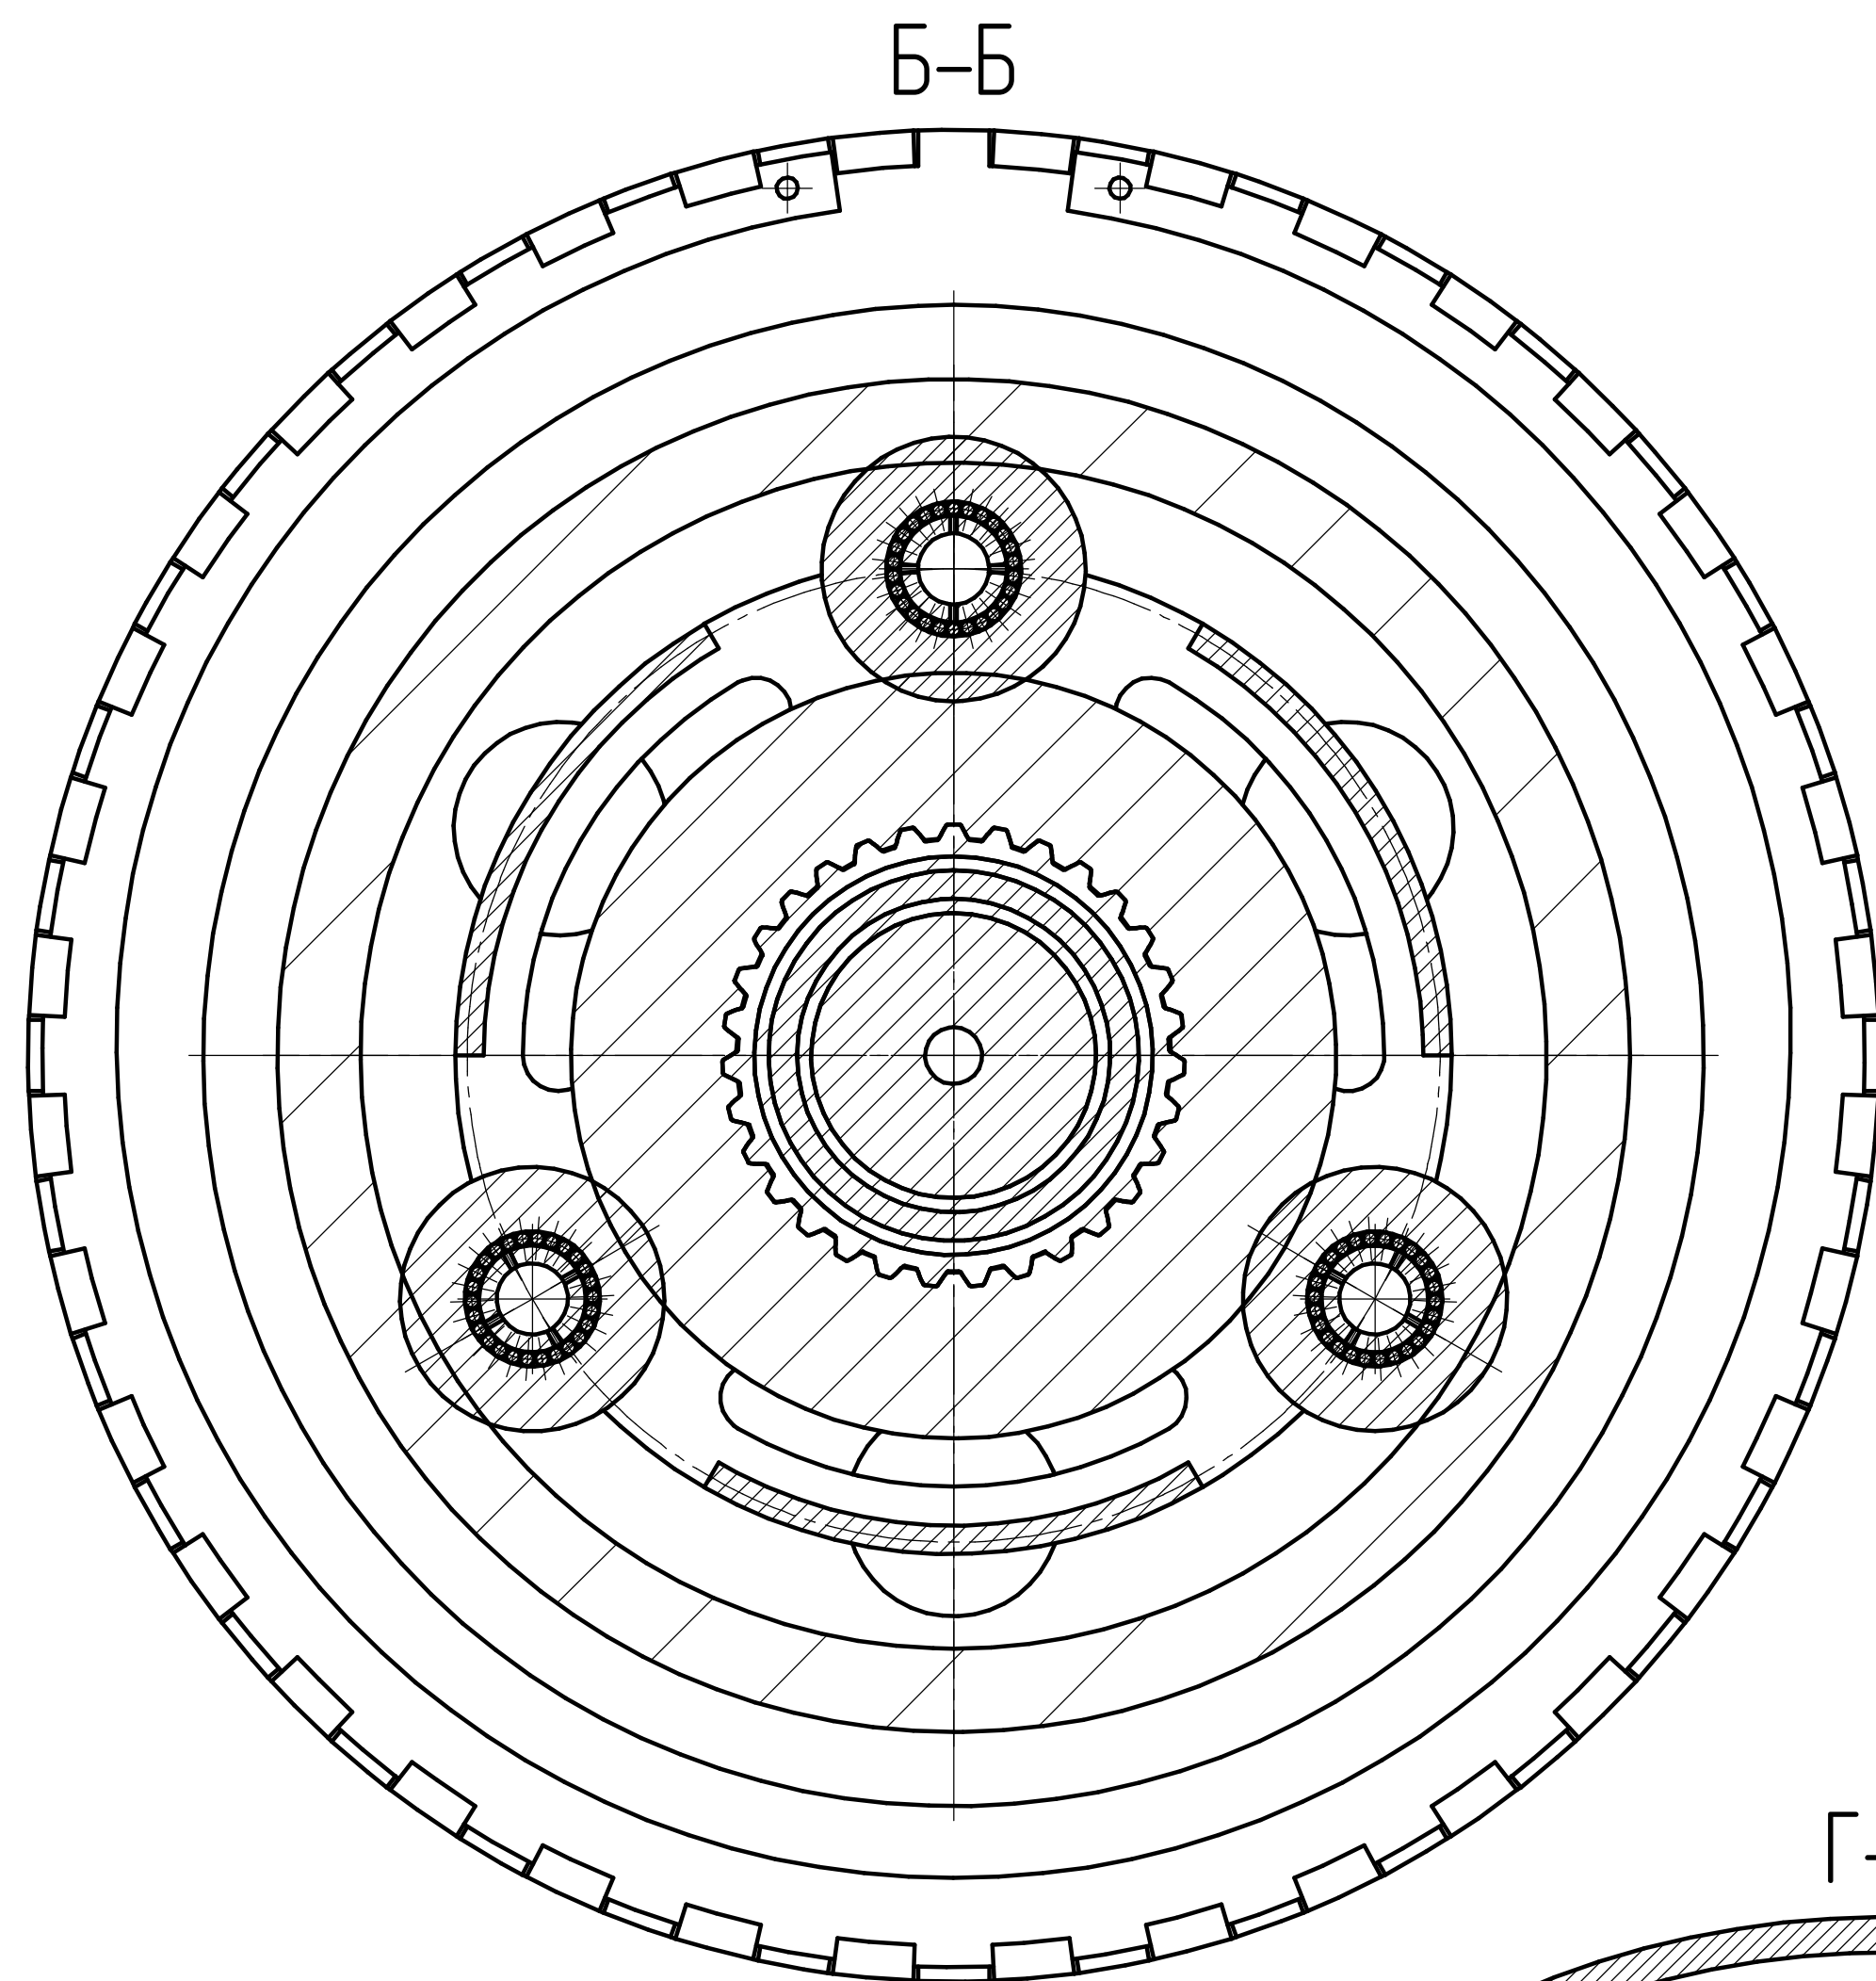

КПСМ 09.2026.05.000 СБ

КМПУС-ЭП 123 Учредителю © 2024 ООО "АНОИ-Служба проектных". Разрешено копировать, распространять, публиковать, использовать в коммерческих целях. Все права защищены.

Имя	№ докум.	Подп.	Имя	№ докум.	Подп.	Имя	№ докум.	Подп.	Имя	№ докум.	Подп.

Имя	№ докум.	Подп.	Имя	№ докум.	Подп.	Имя	№ докум.	Подп.	Имя	№ докум.	Подп.

КПСМ 09.2026.05.000 СБ	Лист
	4